

Pisos

CÓD.	PRODUTO	ÁREA
P01	Porcelanato Santorini OFW NAT	197,67
P02	Porcelanato Santorini SGR HARD	96,01
PP01	Pedra portuguesa branca	150,10
-	Corredor Lateral Externo — P02 ou PI01 (a definir)	23,93
Total geral		467,71

Rodapés

CÓD.	RODAPÉ (H = 8 CM)	LÍQUIDO
R01	Santorini OFW NAT — mesmo piso P01	159,10
R02	Santorini SGR HARD — mesmo piso P02	30,04
Total		189,14

Trechos e memória de cálculo nas folhas 03/06 e 04/06. Sem rodapé em PP01 e no Corredor Lateral Externo.

duas design & arq

FOLHA

01/06

CADERNO DE DETALHAMENTO DE REVESTIMENTO DE PISO 01/02

TIPO

Planta de especificação de pisos

OBRA

Design de interiores de casa unifamiliar térrea

CLIENTES

Ivan e Carol

ENDEREÇO

Nova Odessa, SP

ARQ. RESPONSÁVEL

Lidiane Barbosa
CAU A290220-6

ARQ. CORRESPONSÁVEL

Isadora Ferrari
CAU A269382-8

DATA

26/09/2026

REVISÃO

Nº 00

ESCALA

1/125


CONFERIR AS MEDIDAS NO LOCAL

LEGENDA

- P01 Santorini OFW NAT
90 × 90
- P02 Santorini SGR
HARD 90 × 90
- PP01 Pedra portuguesa
branca
- A definir: P02 ou PI01
(intertravado
drenante)
- Área verde (sem piso)
- Piscina
- Transição de piso
(folha 05/06)
- Soleira mármore
Itaúnas, baguete 5 cm
(detalhe D3)
- Vão de porta
- Divisa do lote


ESCALA

1/125

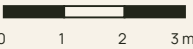

Imprimir em A3 sem ajuste de escala.

² Quarto Casal e Closet Casal pela geometria do DWG (16,28 + 12,25 = 28,53 m²). No quadro, o conjunto adota 28,70 m² (maior valor, Prefeitura).

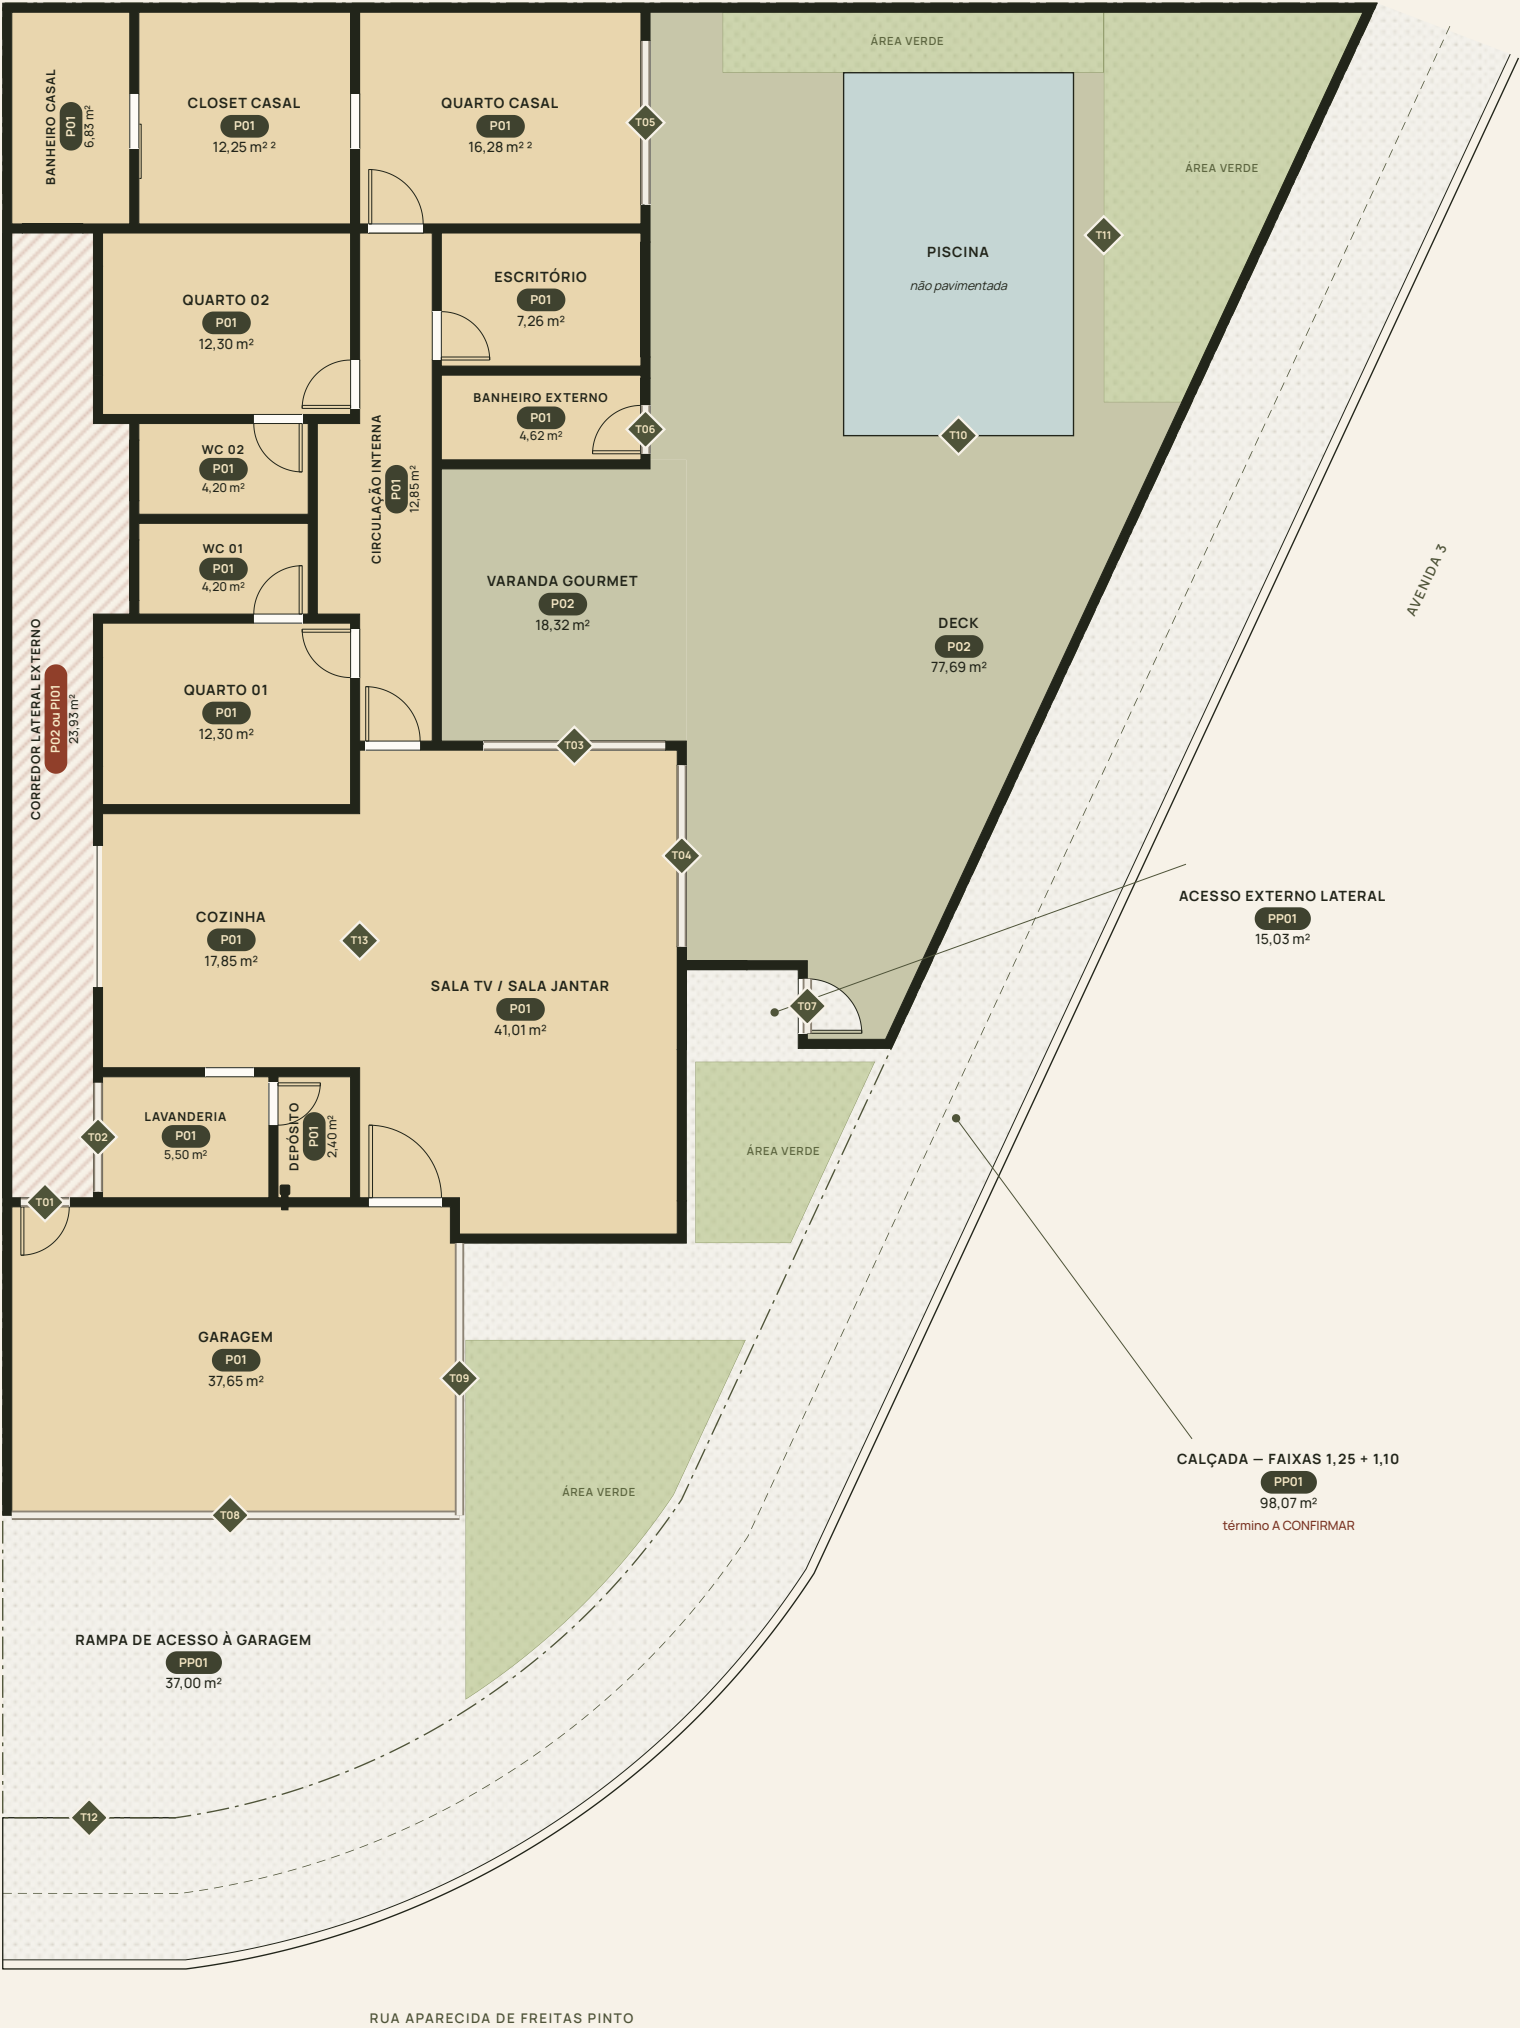

Quadro de pisos

CÓD.	AMBIENTE	PRODUTO	FABRICANTE	FORMATO	ACABAMENTO	REJUNTE	ÁREA M²	CONTROLE	
P01 · PORCELANATO SANTORINI OFW NAT – PORTINARI									
P01	Quarto Casal + Closet Casal	Porcelanato Santorini OFW NAT	Portinari	90 × 90 cm	Natural (NAT)	Corda · junta seca	28,70	Arquivo	Informado
P01	Banheiro Casal	Porcelanato Santorini OFW NAT	Portinari	90 × 90 cm	Natural (NAT)	Corda · junta seca	6,83	Arquivo	
P01	Quarto 01	Porcelanato Santorini OFW NAT	Portinari	90 × 90 cm	Natural (NAT)	Corda · junta seca	12,30	Arquivo	Informado
P01	WC 01	Porcelanato Santorini OFW NAT	Portinari	90 × 90 cm	Natural (NAT)	Corda · junta seca	4,20	Arquivo	Informado
P01	Quarto 02	Porcelanato Santorini OFW NAT	Portinari	90 × 90 cm	Natural (NAT)	Corda · junta seca	12,30	Arquivo	Informado
P01	WC 02	Porcelanato Santorini OFW NAT	Portinari	90 × 90 cm	Natural (NAT)	Corda · junta seca	4,20	Arquivo	Informado
P01	Escritório	Porcelanato Santorini OFW NAT	Portinari	90 × 90 cm	Natural (NAT)	Corda · junta seca	7,26	Arquivo	Informado
P01	Banheiro Externo	Porcelanato Santorini OFW NAT	Portinari	90 × 90 cm	Natural (NAT)	Corda · junta seca	4,62	Arquivo	
P01	Circulação Interna (inclui nicho de marcenaria)	Porcelanato Santorini OFW NAT	Portinari	90 × 90 cm	Natural (NAT)	Corda · junta seca	12,85	Arquivo	Obra
P01	Cozinha	Porcelanato Santorini OFW NAT	Portinari	90 × 90 cm	Natural (NAT)	Corda · junta seca	17,85	Arquivo	Informado
P01	Sala TV / Sala Jantar (integradas)	Porcelanato Santorini OFW NAT	Portinari	90 × 90 cm	Natural (NAT)	Corda · junta seca	41,01	Arquivo	Informado
P01	Lavanderia	Porcelanato Santorini OFW NAT	Portinari	90 × 90 cm	Natural (NAT)	Corda · junta seca	5,50	Arquivo	Informado
P01	Depósito	Porcelanato Santorini OFW NAT	Portinari	90 × 90 cm	Natural (NAT)	Corda · junta seca	2,40	Arquivo	Informado
P01	Garagem	Porcelanato Santorini OFW NAT	Portinari	90 × 90 cm	Natural (NAT)	Corda · junta seca	37,65	Arquivo	
Subtotal P01							197,67		
P02 · PORCELANATO SANTORINI SGR HARD – PORTINARI									
P02	Varanda Gourmet	Porcelanato Santorini SGR HARD	Portinari	90 × 90 cm	HARD (antiderrapante)	Corda · junta seca	18,32	Arquivo	
P02	Deck (inclui faixas sob beiral)	Porcelanato Santorini SGR HARD	Portinari	90 × 90 cm	HARD (antiderrapante)	Corda · junta seca	77,69	Arquivo	Informado
Subtotal P02							96,01		
PP01 · PEDRA PORTUGUESA BRANCA									
PP01	Rampa de acesso à garagem	Pedra portuguesa branca	—	A CONFIRMAR	A CONFIRMAR	A CONFIRMAR	37,00	Informado	
PP01	Acesso externo lateral (até P03)	Pedra portuguesa branca	—	A CONFIRMAR	A CONFIRMAR	A CONFIRMAR	15,03	Arquivo	Obra
PP01	Calçada — faixas de acesso e livre (2,35 m)	Pedra portuguesa branca	—	A CONFIRMAR	A CONFIRMAR	A CONFIRMAR	98,07	Arquivo	Obra
Subtotal PP01							150,10		
A DEFINIR — P02 (SANTORINI SGR HARD) OU PI01 (PISO INTERTRAVADO DRENANTE)									
P02/PI01	Corredor Lateral Externo	A DEFINIR: P02 ou PI01	Portinari / A CONFIRMAR	90 × 90 cm ou A CONFIRMAR	HARD ou drenante	Corda ou A CONFIRMAR	23,93	Informado	Obra
Subtotal a definir (P02 ou PI01)							23,93		
TOTAL GERAL (P01 + P02 + PP01 + a definir) — cada ambiente contado uma vez							467,71		

ESPECIFICAÇÃO DOS PORCELANATOS – DADOS DO FABRICANTE

P01	Santorini OFW NAT 90 × 90							
DESCRIÇÃO	Porcelanato esmaltado Santorini OFW NAT (Off White), borda retificada							
FABRICAÇÃO	900 × 900 mm · espessura 7,0 mm · monocalibre							
EMBALAGEM	3 peças / 2,43 m² por caixa							
USO	áreas internas (Cód. Portinari, variação V e classe de uso: A CONFIRMAR na ficha)							
JUNTA	junta seca (fabricante)							
REJUNTE	cor Corda (sugerida pelo fabricante) · proposta: argamassa de rejuntamento tipo II, NBR 14992, em WCs, banheiros, cozinha e lavanderia; tipo I nas áreas secas							

P02	Santorini SGR HARD 90 × 90							
DESCRIÇÃO	Porcelanato esmaltado Santorini SGR HARD (Stone Gray, cinza), cód. 62928, borda retificada							
FABRICAÇÃO	900 × 900 mm · espessura 8,0 mm · monocalibre							
EMBALAGEM	2 peças / 1,62 m² por caixa							
USO	USO 6 (residencial e comercial de tráfego intenso) · variação V3 · interno e externo							
JUNTA	junta seca (fabricante)							
REJUNTE	cor Corda (sugerida pelo fabricante) · proposta: argamassa de rejuntamento tipo II, NBR 14992 (área externa)							

CRITÉRIOS

- 1

Dados técnicos dos porcelanatos pelos links do fabricante informados pela arquitetura (Portinari). Conferir na ficha técnica vigente antes da compra.
- 2

Rejunte: cor Corda e junta seca, conforme o fabricante. O tipo da argamassa de rejuntamento (NBR 14992) é proposta e depende da aprovação da arquitetura.
- 3

Áreas pela face interna das paredes, sem soleiras. Nas divergências entre documentos, adotado o maior valor.
- 4

Deck com as faixas de 1,00 m sob o beiral. Piscina não pavimentada.
- 5

Calçada: faixas 1,25 + 1,10 = 2,35 m, sem o meio-fio (com ele: 104,54 m²). Término junto à Av. 3 A CONFIRMAR. Rampa: valor informado; pela geometria, 34,61 m².
- 6

Quantitativos líquidos, sem perdas de compra. Níveis não considerados.

Controle dos dados: Arquivo confirmado no arquivo · Informado informado pela arquitetura · Obra conferir em obra · Decisão decisão da arquitetura.



duas
design
& arq

FOLHA

02/06

CADERNO DE DETALHAMENTO DE REVESTIMENTO DE PISO 01/02

T I P O

Quadro de pisos

OBRA

Design de interiores de casa unifamiliar térrea

CLIENTES
Ivan e Carol

ENDEREÇO
Nova Odessa, SP

ARQ. RESPONSÁVEL
Lidiane Barbosa
CAU A290220-6

ARQ. CORRESPONSÁVEL
Isadora Ferrari
CAU A269382-8

DATA
26/09/2026

REVISÃO
Nº 00

ESCALA
Sem escala

CONFERIR AS MEDIDAS NO LOCAL

- **R01** Rodapé Santorini OFW NAT, h = 8 cm
- **R02** Rodapé Santorini SGR HARD, h = 8 cm
- Início / fim de trecho de rodapé
- Vão de porta descontado – largura do DWG (m)
- Face de parede sem rodapé

ESCALA

A horizontal number line is shown with tick marks at 0, 1, 2, and 3. The segment between 1 and 2 is shaded in light blue.

BANHEIRO CASAL
R01
10,00 m

CLOSET CASAL
R01
12,20 m

QUARTO CASAL
R01
11,80 m

QUARTO 02
R01
12,60 m

WC 02
R01
7,80 m

WC 01
R01
7,80 m

QUARTO 01
R01
12,60 m

COZINHA
R01
11,90 m

LAVANDERIA
R01
6,20 m

DEPÓSITO
R01
5,70 m

GARAGEM
R01
11,10 m

ESCRITÓRIO
R01
10,20 m

BANHEIRO EXTERNO
R01
8,60 m

VARANDA GOURMET
R02
9,00 m

SALA TV / SALA JANTAR
R01
14,20 m

PISCINA
sem rodapé na borda

DECK
R02
21,04 m

CORREDOR LATERAL EXTERNO
sem rodapé
R02 ou P01

CIRCULAÇÃO INTERNA
R01
16,40 m

Portas: P01, P02, P03, P04, P05, P06, P07, P08, P09, P10, P11

Dimensões das portas: 0,80, 0,90, 1,20, 1,80, 2,70, 3,00, 4,20

Outros detalhes: lateral aberta - sem rodapé, frente aberta - sem rodapé

medidas em metros

CÓD.	VÃO DWG	QUADRO ESQ.	QTD.
P01	1,20	1,20	1
P02	0,80	0,90	1
P03	0,90	0,90	1
P04	4,20	4,20	1
P05	3,00	3,00	2
P06	0,70 / 0,80 / 0,90	0,90	9
P07	1,80	1,80	1
P08	0,90	1,00	1
P09	0,90	1,00	1
P10	2,70	2,50	1
P11	0,80	0,90	1

metros lineares

CÓD.	RODAPÉ (H = 8 CM)	LÍQUIDO
R01	Santorini OFW NAT	159,10
R02	Santorini SGR HARD	30,04
Total		189,14

duas
design
& gra

duas
design
& arg

FOLHA

03/06

CADERNO DE DETALHAMENTO DE REVESTIMENTO DE
PISO 01/02

TIPO

Planta de rodapés

OBRA

Design de interiores de casa unifamiliar térrea

CLIENTES
Ivan e Carol

ENDEREÇO
Nova Odessa, SP

ARQ. RESPONSÁVEL
Lidiane Barbosa
CAU A290220-6

ARQ. CORRESPONSÁVEL
Isadora Ferrari
CAU A269382-8

DATA
26/09/2026

REVISÃO
Nº 00

ESCALA
1/100

CONFERIR AS MEDIDAS NO LOCAL

Memória de cálculo dos rodapés

CÓD.	AMBIENTE	TRECHOS DE PAREDE (M) – POSIÇÃO NA PLANTA	SOMA	VÃOS DE PORTA DESCONTADOS (DWG)	VÃOS	LÍQUIDO	CONTROLE
R 01 · RODAPÉ PORCELANATO SANTORINI OFW NAT · H = 8 CM							
R01	Quarto Casal	inf. 4,65 + dir. 3,50 + sup. 4,65 + esq. 3,50	16,30	P06 0,90 + P10 2,70 + P08 0,90	4,50	11,80	Arquivo
R01	Closet Casal Trechos atrás de marcenaria: conferir com o projeto de marcenaria	inf. 3,50 + dir. 3,50 + sup. 3,50 + esq. 3,50	14,00	P08 0,90 + P09 0,90	1,80	12,20	Arquivo
R01	Banheiro Casal	inf. 1,95 + dir. 3,50 + sup. 1,95 + esq. 3,50	10,90	P09 0,90	0,90	10,00	Arquivo
R01	Quarto 02	inf. 4,10 + dir. 3,00 + sup. 4,10 + esq. 3,00	14,20	P06 0,80 + P06 0,80	1,60	12,60	Arquivo
R01	WC 02	inf. 2,80 + dir. 1,50 + sup. 2,80 + esq. 1,50	8,60	P06 0,80	0,80	7,80	Arquivo
R01	WC 01	inf. 2,80 + dir. 1,50 + sup. 2,80 + esq. 1,50	8,60	P06 0,80	0,80	7,80	Arquivo
R01	Quarto 01	inf. 4,10 + dir. 3,00 + sup. 4,10 + esq. 3,00	14,20	P06 0,80 + P06 0,80	1,60	12,60	Arquivo
R01	Escritório	inf. 3,30 + dir. 2,20 + sup. 3,30 + esq. 2,20	11,00	P06 0,80	0,80	10,20	Arquivo
R01	Banheiro Externo	inf. 3,30 + dir. 1,40 + sup. 3,30 + esq. 1,40	9,40	P11 0,80	0,80	8,60	Arquivo
R01	Circulação Interna Nicho (futura marcenaria) com piso e rodapé, conforme informado	inf. 1,20 + dir. 8,40 + sup. 1,20 + esq. sup. 3,15 + nicho sup. 0,70 + nicho esq. 3,15 + nicho inf. 0,70 + esq. inf. 2,10	20,60	P06 0,90 + P06 0,80 + P06 0,90 + P06 0,80 + P06 0,80	4,20	16,40	Arquivo Informado
R01	Cozinha	inf. 4,25 + dir. 4,20 + sup. 4,25 + esq. 4,20	16,90	P06 0,80 + P04 4,20	5,00	11,90	Arquivo Informado
R01	Lavanderia	inf. 2,75 + dir. 2,00 + sup. 2,75 + esq. 2,00	9,50	P06 0,80 + P06 0,70 + P07 1,80	3,30	6,20	Arquivo
R01	Depósito	inf. 1,20 + dir. 2,00 + sup. 1,20 + esq. 2,00	6,40	P06 0,70	0,70	5,70	Arquivo
R01	Sala TV / Sala Jantar J01 (peitoril 0,50) não descontada	inf. esq. 1,65 + recuo 0,60 + inf. dir. 3,60 + dir. 8,00 + sup. 5,25 + esq. 7,40	26,50	P01 1,20 + P05 3,00 + P05 3,00 + P06 0,90 + P04 4,20	12,30	14,20	Arquivo Informado
R01	Garagem Frente (7,40) e lateral direita (4,50) abertas no DWG: sem rodapé	esq. 5,10 + sup. 7,25 + pilar dir. 0,60 + pilar inf. 0,15	13,10	P02 0,80 + P01 1,20	2,00	11,10	Arquivo
Subtotal R01						159,10	
R 02 · RODAPÉ PORCELANATO SANTORINI SGR HARD · H = 8 CM							
R02	Varanda Gourmet Lado direito aberto para o deck: sem rodapé	inf. 4,05 + esq. 4,50 + sup. 3,45	12,00	P05 3,00	3,00	9,00	Arquivo
R02	Deck (inclui faixas sob beiral) Sem rodapé junto à piscina e às áreas verdes	fachada Q. Casal/Escr./B. Ext. 7,40 + muro sup. 1,20 + fachada Sala 3,63 + muro inf. 2,00 + portão P03 + batentes 1,30 + muro portão 1,29 + muro de divisa (diag.) 11,61	28,44	P10 2,70 + P11 0,80 + P05 3,00 + P03 0,90	7,40	21,04	Arquivo Informado
Subtotal R02						30,04	
TOTAL GERAL DE RODAPÉS (R01 + R02)						189,14	

REGRA DE CÁLCULO

- 1

Rodapé líquido = soma dos trechos de parede – vãos de porta aplicáveis. Janelas não são descontadas. Cada face de parede entra uma única vez; as duas faces de uma mesma parede pertencem a ambientes diferentes.
- 2

Material do rodapé = piso do ambiente: P01 → R01 (Santorini OFW NAT); P02 → R02 (Santorini SGR HARD). Altura 8 cm (informada), rejunte igual ao do piso. Sem rodapé em PP01 (rampa, acesso externo e calçada) e no Corredor Lateral Externo.
- 3

Trechos sem rodapé: faces abertas da garagem (frente 7,40 e lateral 4,50), lado aberto da varanda, bordas da piscina e limites com áreas verdes.
- 4

Vãos pelo DWG (orientação da arquitetura). P04 (4,20) não está no DWG: descontada como passagem entre Cozinha e Sala, conforme informado. Com as larguras do Quadro de Esquadrias Rev. 01 o líquido de R01 seria 157,10 m e o de R02, 30,14 m.
- 5

Circulação Interna: inclui o nicho de 0,70 × 3,15 m (futura marcenaria), com piso e rodapé, conforme informado.
- 6

Metros lineares líquidos, sem perdas de corte ou de compra.

Controle dos dados: Arquivo confirmado no arquivo · Informado informado pela arquitetura · Obra conferir em obra · Decisão decisão da arquitetura.



FOLHA

04/06

CADERNO DE DETALHAMENTO DE REVESTIMENTO DE PISO 01/02

T I P O

Memória de cálculo dos rodapés

OBRA
Design de interiores de casa unifamiliar térrea

CLIENTES
Ivan e Carol

ENDEREÇO
Nova Odessa, SP

ARQ. RESPONSÁVEL
Lidiane Barbosa
CAU A290220-6

ARQ. CORRESPONSÁVEL
Isadora Ferrari
CAU A269382-8

DATA
26/09/2026

REVISÃO
Nº 00

ESCALA
Sem escala

CONFERIR AS MEDIDAS NO LOCAL

Transições e pendências

CÓD.	PORTA	ENCONTRO DE PISOS	SOLUÇÃO	SOLEIRA M	CONTROLE
T01	P02	Garagem (P01) / Corredor Lateral Externo (P02 ou PI01)	Soleira mármore Itaúnas, baguete 5 cm × comprimento do vão (0,80 m).	0,80	Informado
T02	P07	Lavanderia (P01) / Corredor Lateral Externo (P02 ou PI01)	Soleira mármore Itaúnas, baguete 5 cm × comprimento do vão (1,80 m). Compatibilizar com o trilho embutido (esquadrias, notas 3 e 10).	1,80	Informado
T03	P05	Sala TV / Sala Jantar (P01) / Varanda Gourmet (P02)	Soleira mármore Itaúnas, baguete 5 cm × comprimento do vão (3,00 m). Compatibilizar com o trilho embutido.	3,00	Informado
T04	P05	Sala TV / Sala Jantar (P01) / Deck (P02)	Soleira mármore Itaúnas, baguete 5 cm × comprimento do vão (3,00 m). Compatibilizar com o trilho embutido.	3,00	Informado
T05	P10	Quarto Casal (P01) / Deck (P02)	Soleira mármore Itaúnas, baguete 5 cm × comprimento do vão (2,70 m). Compatibilizar com o trilho da veneziana de correr.	2,70	Informado
T06	P11	Banheiro Externo (P01) / Deck (P02)	Soleira mármore Itaúnas, baguete 5 cm × comprimento do vão (0,80 m).	0,80	Informado
T07	P03	Deck (P02) / Acesso externo (PP01)	Soleira mármore Itaúnas, baguete 5 cm × comprimento do vão (0,90 m).	0,90	Informado
T08	—	Garagem (P01) / Rampa (PP01) — frente aberta	Soleira mármore Itaúnas, baguete 5 cm × comprimento do vão (7,40 m, linha y = 15,036).	7,40	Informado
T09	—	Garagem (P01) / Acesso externo (PP01) — lateral aberta	Soleira mármore Itaúnas, baguete 5 cm × comprimento do vão (4,50 m).	4,50	Informado
T10	—	Deck (P02) / Piscina	Borda da piscina e arremate não documentados: A CONFIRMAR.	—	Decisão
T11	—	Deck (P02) e PP01 / áreas verdes	Contenção/arremate entre piso e jardim não documentado: A CONFIRMAR.	—	Decisão
T12	—	Rampa (PP01) / Calçada (PP01) — divisa	Mesmo material: sem soleira. Havendo desnível: perfil metálico (mesmo material, somente com desnível).	—	Informado
T13	P04	Cozinha (P01) / Sala TV / Sala Jantar (P01)	Mesmo material: sem soleira. Havendo desnível: perfil metálico (mesmo material, somente com desnível). Posição do trilho de P04 A CONFIRMAR.	—	Informado
T14	P06/P08/P09	Portas internas (P01 / P01)	Mesmo material: sem soleira. Havendo desnível: perfil metálico (mesmo material, somente com desnível).	—	Informado
TOTAL DE SOLEIRAS — mármore Itaúnas, baguete 5 cm (9 trechos)				24,90	

PENDÊNCIAS — DECISÃO DA ARQUITETURA

- 1
- Corredor Lateral Externo (23,93 m², incluído no total): definir entre P02 (Santorini SGR HARD) e PI01 (piso intertravado drenante). Dimensões, espessura, cor e resistência do PI01: A CONFIRMAR (anúncio não acessível na elaboração). Sem rodapé.
- 2
- P02: o produto do link é o Santorini SGR HARD (SGR = Stone Gray, cinza), não uma versão Off White. Confirmar a cor para a varanda, o deck e o rodapé R02.
- 3
- P01 (Santorini OFW NAT): confirmar na ficha técnica o código Portinari, a variação de tonalidade e a classe de uso (as fontes consultadas divergem entre USO 5 e USO 6).
- 4
- Rejunte: aprovar o tipo proposto (NBR 14992 tipo II em áreas externas e molhadas; tipo I em áreas secas), a marca e a largura da junta, conforme o manual de assentamento Portinari.
- 5
- PP01: formato/granulometria da pedra portuguesa branca, assentamento e rejunte.
- 6
- Calçada: término junto à Av. 3 (linhas abertas no DWG). A Prefeitura indica concreto vassourado na faixa de acesso e grama na faixa de serviço; confirmar a exigência municipal.
- 7
- Acesso externo lateral (15,03 m²): a Prefeitura indica concreto vassourado; a planta do caderno de esquadrias mostra grama com pisantes. Confirmar o limite da pedra portuguesa.
- 8
- Rodapé em áreas molhadas: compatibilizar com o Caderno 02/02 (revestimento de parede).
- 9
- Soleiras de mármore × trilhos embutidos de P05, P07 e P10, e posição do trilho de P04 (não desenhada no DWG).
- 10
- Borda da piscina e arremates entre piso e jardim — não documentados.

PENDÊNCIAS — CONFERÊNCIA EM OBRA

- 11
- Vãos executados × vãos do DWG × Quadro de Esquadrias Rev. 01: 13 das 20 portas têm largura diferente. Descontos de rodapé e comprimentos de soleira pelo DWG.
- 12
- Áreas divergentes adotadas pelo maior valor: Quarto Casal + Closet 28,70; Banheiro Casal 6,83; Banheiro Externo 4,62; Circulação 12,85; Garagem 37,65; Varanda 18,32; Rampa 37,00; Corredor Lateral Externo 23,93.
- 13
- Rampa: limite direito considerado no alinhamento da garagem; há guia/muro 0,10 m adiante.
- 14
- Rodapé atrás de marcenaria (closet, nicho da circulação, armários): conferir com o projeto de marcenaria.
- 15
- Tubeamento junto à parede superior da garagem: recortar o rodapé em obra.
- 16
- Todas as medidas devem ser conferidas no local antes da compra.

CRITÉRIOS DE TRANSIÇÃO (INFORMADOS PELA ARQUITETURA)

- 1
- Mesmo produto/material, apenas com mudança de nível: perfil metálico.
- 2
- Troca de material: soleira de mármore Itaúnas, tipo baguete, com 5 cm de profundidade pelo comprimento do vão.
- 3
- Níveis não documentados neste caderno. Onde houver desnível entre pisos iguais, aplicar o critério 1.
- 4
- Detalhes ilustrativos: perfil metálico (D2), soleira baguete (D3) e trilho embutido (D4) na folha 06/06.

OBSERVAÇÕES

- Paginação de piso não faz parte deste caderno. Revestimentos de parede: Caderno 02/02.
- Fonte de títulos substituída pela Outfit (Aloevera Display não disponível).

Controle dos dados:

Arquivo

 confirmado no arquivo ·

Informado

 informado pela arquitetura ·

Obra

 conferir em obra ·

Decisão

 decisão da arquitetura.



duas
design
& arq

FOLHA

05/06

CADERNO DE DETALHAMENTO DE REVESTIMENTO DE PISO 01/02

T I P O

Transições e pendências

OBRA
Design de interiores de casa unifamiliar térrea

CLIENTES
Ivan e Carol

ENDEREÇO
Nova Odessa, SP

ARQ. RESPONSÁVEL
Lidiane Barbosa
CAU A290220-6

ARQ. CORRESPONSÁVEL
Isadora Ferrari
CAU A269382-8

DATA
26/09/2026

REVISÃO
Nº 00


ESCALA
Sem escala

CONFERIR AS MEDIDAS NO LOCAL

Detalhes de rodapé e transições


D1 Rodapé em porcelanato — h = 8 cm

Corte ilustrativo · sem escala

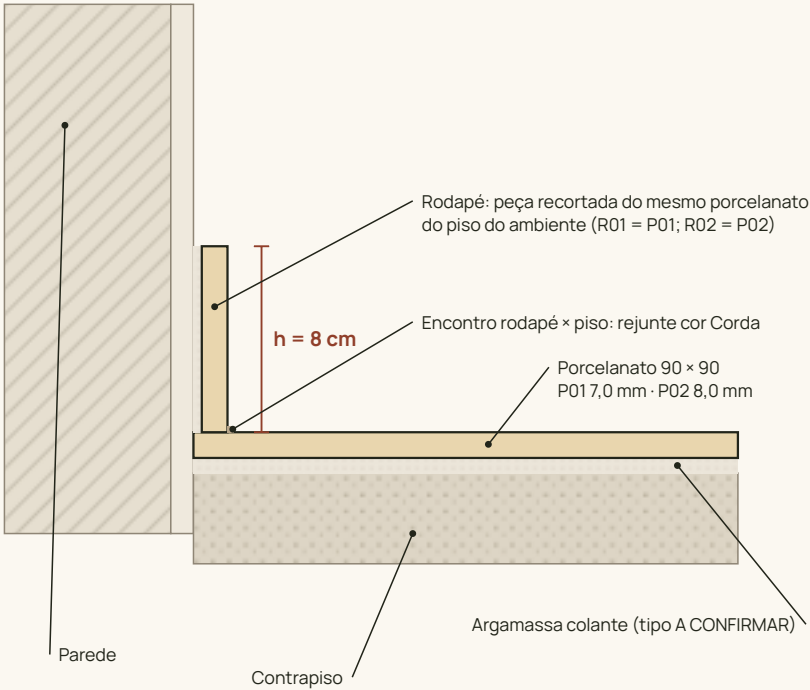

D2 Perfil metálico em L — mesmo material com desnível


Corte ilustrativo · sem escala

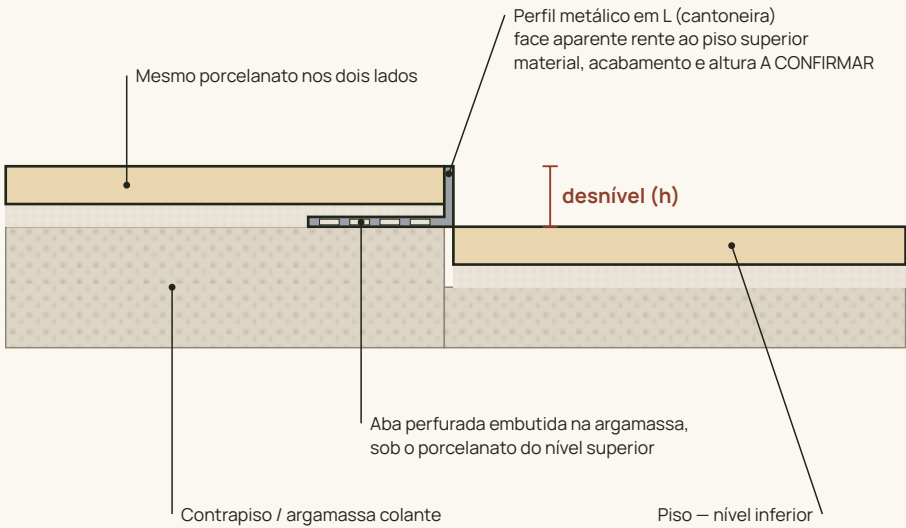


Aplicar somente quando o mesmo material mudar de nível. Níveis não documentados neste caderno.

D3 Soleira baguete — mármore Itaúnas

Corte e planta ilustrativos · sem escala

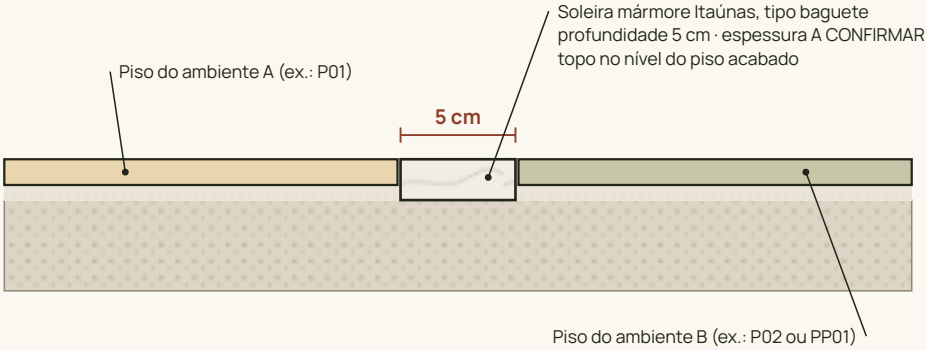


PLANTA

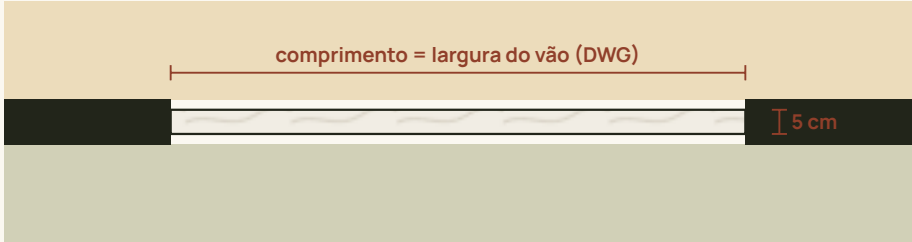

D4 Trilho de porta de correr embutido no piso

Corte ilustrativo · sem escala

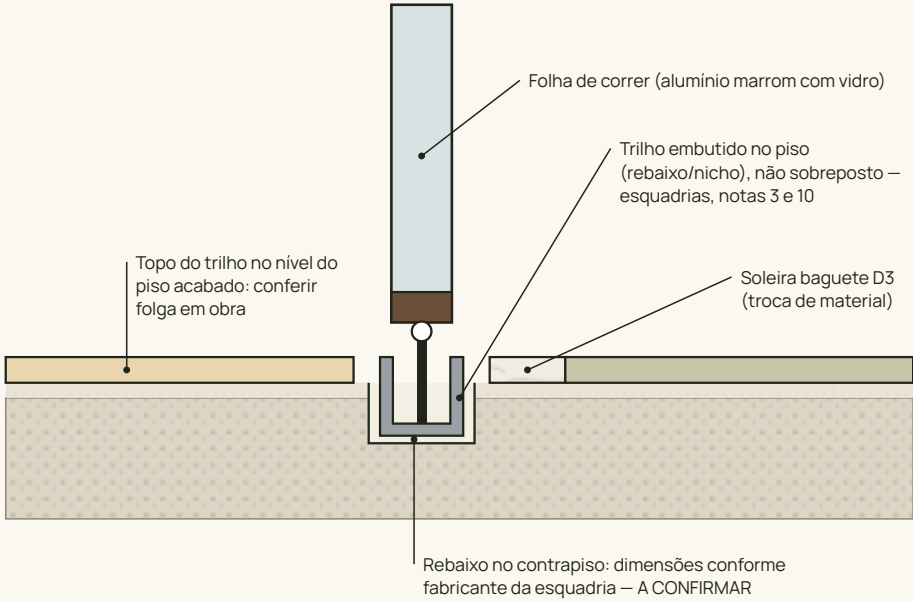

Aplica-se a P04, P05 e P07 (caderno de esquadrias), P10: tipo de trilho A CONFIRMAR. Nas portas externas, compatibilizar o trilho com a soleira baguete.

ONDE SE APLICA

- D1 Todos os rodapés R01 e R02 (folhas 03/06 e 04/06).
- D2 Encontros do mesmo material com desnível (critério 1 da folha 05/06). Níveis não documentados neste caderno.
- D3 Trocas de material T01 a T09 — 24,90 m de soleira (folha 05/06).
- D4 Portas de correr P04, P05 e P07; P10 A CONFIRMAR. Nas portas externas, compatibilizar o trilho com a soleira D3.

Desenhos ilustrativos, sem escala. Cotas indicadas: rodapé 8 cm e soleira 5 cm (informados); espessuras do porcelanato conforme o fabricante. Demais dimensões: A CONFIRMAR.



FOLHA

06/06

CADERNO DE DETALHAMENTO DE REVESTIMENTO DE PISO 01/02

TIPO

Detalhes de rodapé e transições

OBRA

Design de interiores de casa unifamiliar térrea

CLIENTES

Ivan e Carol

ENDEREÇO

Nova Odessa, SP

ARQ. RESPONSÁVEL

Lidiane Barbosa
CAU A290220-6

ARQ. CORRESPONSÁVEL

Isadora Ferrari
CAU A269382-8

DATA

26/09/2026

REVISÃO

Nº 00

ESCALA

Sem escala

CONFERIR AS MEDIDAS NO LOCAL