




LEGENDA

- RP01** Pedra Moledo
Pedreira (compra à parte)
- RP02** Porcelanato
Santorini OFW NAT
Portinari
- RP03** Porcelanato
Confete WH NAT
CEUSA · cód. 5041209A
- RP04** Porcelanato
Confete PK NAT (Pink)
CEUSA · cód. 5041210A
- RP05** Revestimento
Fatto Oliva AC
Decortiles · SC 8068139
- RP06** Travertino Rock
Face
Pedreira (compra à parte)
- RP07** Cerâmica simples
Eliane · SC 8039383
- Face revestida (faixa
gráfica, fora de escala)
- Elevação: código / folha

ESCALA

1/75

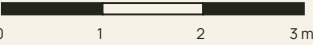

Imprimir em A3 sem ajuste de escala.

Revestimentos

		áreas líquidas em m²
RP01	Pedra Moledo	32,93
RP02	Porcelanato Santorini OFW NAT	32,16
RP03	Porcelanato Confete WH NAT	5,41
RP04	Porcelanato Confete PK NAT (Pink)	8,07
RP05	Revestimento Fatto Oliva AC	4,33
RP06	Travertino Rock Face	6,51
RP07	Cerâmica simples	23,02
Total		112,44

Elevações

		escala 1/50
E01	Fachada sul da Sala	03/05
E02	Fachada leste da Sala	03/05
E03	Sala — parede da TV	03/05
E04	Banheiro Casal — box planejado	04/05
E05	WC 02 — box planejado	04/05
E06	WC 01 — box planejado	04/05
E07	Banheiro Externo — box planejado	04/05
E08	Lavanderia — parede inferior	05/05
E09	Cozinha — paredes esquerda e superior	05/05
E10	Cozinha — balcão (mureta)	05/05
E11	Varanda Gourmet — parede esquerda e churrasqueira	05/05
E12	Churrasqueira — lateral esquerda	05/05



FOLHA

01/05

CADERNO DE DETALHAMENTO DE REVESTIMENTO DE PAREDE 02/02

T I P O

Planta de revestimentos de parede

OBRA
Design de interiores de casa unifamiliar térrea

CLIENTES
Ivan e Carol

ENDEREÇO
Nova Odessa, SP

ARQ. RESPONSÁVEL
Lidiane Barbosa
CAU A290220-6

ARQ. CORRESPONSÁVEL
Isadora Ferrari
CAU A269382-8

DATA
26/09/2026

REVISÃO
Nº 00

ESCALA
1/75

CONFERIR AS MEDIDAS NO LOCAL

Quadro de revestimentos

ELEV.	AMBIENTE / PANO	LARG. × ALT. (M)	BRUTA	ABERTURAS DESCONTADAS	DESC.	NICHO	LÍQUIDA M²	OBSERVAÇÃO	CONTROLE	
RP01 · PEDRA MOLEDO — PEDREIRA (COMPRA À PARTE)										
E01	Sala — fachada sul (externa) face externa sul, x 11,441 → 15,341	3,90 × 3,20	12,48	—	—	—	12,48	Inclui a face do pilar junto à garagem (0,15 m), conforme imagem enviada	Arquivo	Informado
E02	Sala — fachada leste (externa) face externa leste, y 19,536 → 24,055 (até o muro)	4,52 × 3,20	14,46	J01 2,50×2,50	6,25	—	8,21	Desconta só a janela J01; pedra abaixo, acima e dos lados	Arquivo	Informado
E03	Sala — parede da TV (interna) face interna sul, x 11,591 → 15,191	3,60 × 3,40	12,24	—	—	—	12,24	Parede toda; PD 3,40 m do DWG (imagem cota 3,75 × 3,591 m)	Arquivo	Informado
Subtotal RP01							32,93			
RP02 · PORCELANATO SANTORINI OFW NAT — PORTINARI										
E04	Banheiro Casal lateral do box (0,90 m)	2 × 0,90 × 2,85	5,13	—	—	—	5,13		Arquivo	Informado
E05	WC 02 lateral do box (0,90 m)	2 × 0,90 × 2,85	5,13	—	—	—	5,13		Arquivo	Informado
E06	WC 01 lateral do box (0,90 m)	2 × 0,90 × 2,85	5,13	—	—	—	5,13		Arquivo	Informado
E07	Banheiro Externo lateral do box (0,90 m)	2 × 0,90 × 2,85	5,13	—	—	—	5,13		Arquivo	Informado
E08	Lavanderia parede inferior inteira (divisa com a garagem)	2,75 × 2,85	7,84	—	—	—	7,84		Arquivo	Informado
E10	Cozinha — balcão faces sul e norte da mureta 1,90 × 0,15 (DWG Prefeitura)	2 × 1,90 × 1,00	3,80	—	—	—	3,80		Arquivo	Informado
Subtotal RP02							32,16			
RP03 · PORCELANATO CONFETE WH NAT — CEUSA · CÓD. 5041209A										
E04	Banheiro Casal fundo do box (parede da janela / nicho)	1,95 × 2,85	5,56	J04 1,00×0,60	0,60	0,45	5,41		Arquivo	Informado
Subtotal RP03							5,41			
RP04 · PORCELANATO CONFETE PK NAT (PINK) — CEUSA · CÓD. 5041210A										
E05	WC 02 fundo do box (parede da janela / nicho)	1,50 × 2,85	4,28	J04 1,00×0,60	0,60	0,36	4,04		Arquivo	Informado
E06	WC 01 fundo do box (parede da janela / nicho)	1,50 × 2,85	4,28	J04 1,00×0,60	0,60	0,36	4,04		Arquivo	Informado
Subtotal RP04							8,07			
RP05 · REVESTIMENTO FATTO OLIVA AC — DECORTILES · SC 8068139										
E07	Banheiro Externo fundo do box (parede da janela / nicho)	1,40 × 2,85	3,99	—	—	0,34	4,33		Arquivo	Informado
Subtotal RP05							4,33			
RP06 · TRAVERTINO ROCK FACE — PEDREIRA (COMPRA À PARTE)										
E11	Varanda Gourmet faixa da bancada: 2,75 m, de 0,98 a 1,48 m, junto à churrasqueira	2,75 × 0,50	1,38	—	—	—	1,38	Posição ao longo da parede: junto à churrasqueira, conforme elevação enviada	Arquivo	Informado
E11	Varanda Gourmet — churrasqueira frente (0,90 × 3,40 m)	0,90 × 3,40	3,06	Boca da churrasqueira 0,80×0,80	0,64	—	2,42	Desconta a boca 0,80 × 0,80; posição vertical da boca A CONFIRMAR	Informado	Obra
E12	Varanda Gourmet — churrasqueira lateral esquerda (0,80 × 3,40 m)	0,80 × 3,40	2,72	—	—	—	2,72	Lateral direita encostada na parede do Banheiro Externo: sem revestimento	Informado	
Subtotal RP06							6,51			
RP07 · CERÂMICA SIMPLES — ELIANE FORMA BRANCO AC (FUNDO DA MARCENARIA) — ELIANE · SC 8039383										
E09	Cozinha parede esquerda inteira	4,20 × 2,85	11,97	J02 2,35×0,45	1,06	—	10,91	Altura = PD 2,85 m (paredes inteiras, informado)	Arquivo	Informado
E09	Cozinha parede superior inteira	4,25 × 2,85	12,11	—	—	—	12,11	Altura = PD 2,85 m (paredes inteiras, informado)	Arquivo	Informado
Subtotal RP07							23,02			
TOTAL GERAL DE REVESTIMENTOS DE PAREDE							112,44			

CRITÉRIOS (INFORMADOS)

- 1

Área líquida = largura × altura – aberturas + nicho. Alturas a partir do piso acabado.
- 2

Alturas: Moledo externo 3,20 m; Moledo interno = PD 3,40 m; Santorini 2,85 m e balcão 1,00 m; Confete = PD do local (2,85 m); travertino: faixa 0,98–1,48 m e churrasqueira 3,40 m.
- 3

Box: 0,90 m de cada parede lateral em Santorini em todos os banheiros.
- 4

Nicho em toda a largura da parede da janela (no Banheiro Externo, no fundo do box): altura 0,30 m, profundidade 0,10 m, base a 1,00 m. Interior no mesmo revestimento da parede: acréscimo = base + teto + 2 laterais.
- 5

Dados técnicos pelos links informados (sites consultados indiretamente); conferir na ficha técnica antes da compra.

Controle dos dados:

Arquivo

 confirmado no arquivo ·

Informado

 informado pela arquitetura ·

Obra

 conferir em obra ·

Decisão

 decisão da arquitetura.



FOLHA

02/05

CADERNO DE DETALHAMENTO DE REVESTIMENTO DE PAREDE 02/02

T I P O

Quadro de revestimentos

OBRA
Design de interiores de casa unifamiliar térrea

CLIENTES
Ivan e Carol

ENDEREÇO
Nova Odessa, SP

ARQ. RESPONSÁVEL
Lidiane Barbosa
CAU A290220-6

ARQ. CORRESPONSÁVEL
Isadora Ferrari
CAU A269382-8

DATA
26/09/2026

REVISÃO
Nº 00

ESCALA
Sem escala


CONFERIR AS MEDIDAS NO LOCAL

Elevações — Sala e fachadas

E01

Fachada sul da Sala


Pedra Moledo externa · vista de fora · 1/50 · altura 3,20 m a partir do piso acabado externo

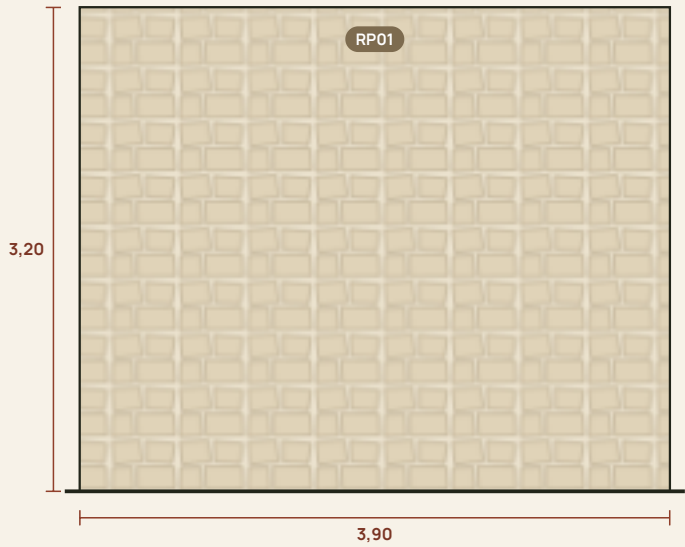

E02

Fachada leste da Sala

Pedra Moledo externa · vista de fora · 1/50 · desconta só a janela J01

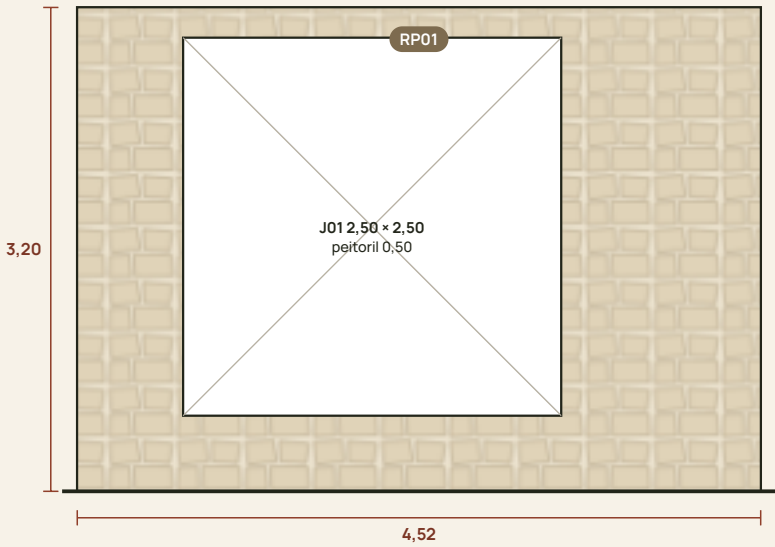

E03

Sala — parede da TV

Pedra Moledo interna · vista de dentro · 1/50 · parede toda, PD 3,40 m (DWG)

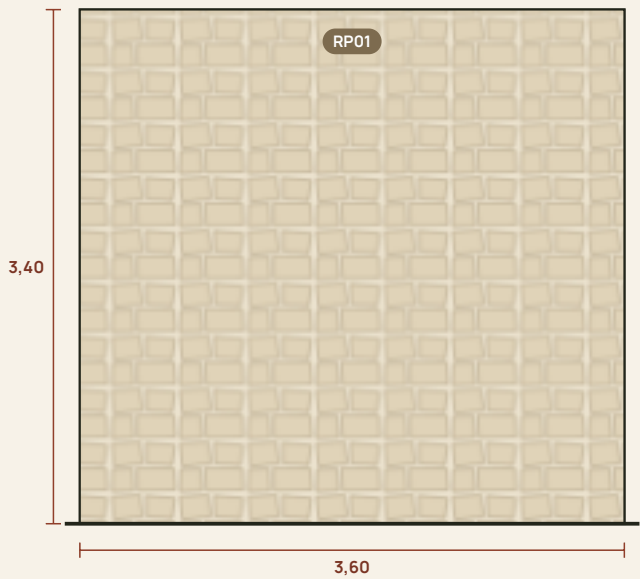


Imagem de referência · Sala TV — ilustrativa; valem as cotas e o quadro.
Observação: a imagem mostra Moledo nas faixas ao lado do painel de madeira; o quantitativo considera a parede toda, conforme informado.

ESPECIFICAÇÃO DOS REVESTIMENTOS

CÓD.	PRODUTO	FABRICANTE	FORMATO	ESPESSURA	ACABAMENTO	REJUNTE
RP01	Pedra Moledo	Pedreira (compra à parte)	A CONFIRMAR	A CONFIRMAR	Natural (pedra)	A CONFIRMAR
RP02	Porcelanato Santorini OFW NAT	Portinari	90 × 90 cm	7,0 mm	Natural (NAT), retificado	Corda · junta seca
RP03	Porcelanato Confete WH NAT	CEUSA · cód. 5041209A	100 × 100 cm	9,0 mm	Natural, retificado	A CONFIRMAR
RP04	Porcelanato Confete PK NAT (Pink)	CEUSA · cód. 5041210A	100 × 100 cm	9,0 mm	Natural, retificado	Sugestão do fabricante: Quartzolit Preto Grafite, Rejuntabras Marfim ou Quartzobras Castor
RP05	Revestimento Fatto Oliva AC	Decortiles · SC 8068139	30 × 90 cm	A CONFIRMAR	Acetinado (AC), V1	A CONFIRMAR
RP06	Travertino Rock Face	Pedreira (compra à parte)	A CONFIRMAR	A CONFIRMAR	Rock face (bruto)	A CONFIRMAR
RP07	Cerâmica simples — Eliane Forma Branco AC (fundo da marcenaria)	Eliane · SC 8039383	30 × 40 cm	6,5 mm	Acetinado, V1	Junta 2 mm (fabricante) · cor A CONFIRMAR

NOTAS

- RP01
- Pedra Moledo, compra em pedreira: formato, espessura, assentamento e rejunte A CONFIRMAR.
- J01
- Janela conforme Quadro de Esquadrias Rev. 01: 2,50 × 2,50 m, peitoril 0,50 m.
- E03
- Largura pela geometria do DWG (3,60 m). A imagem de referência cota 3,75 m e 3,591 m de altura; adotado o PD de 3,40 m (informado).

ESCALA 1 / 50



FOLHA

03/05

CADERNO DE DETALHAMENTO DE REVESTIMENTO DE PAREDE 02/02

T I P O

Elevações — Sala e fachadas

O B R A

Design de interiores de casa unifamiliar térrea

C L I E N T E S

Ivan e Carol

E N D E R E Ç O

Nova Odessa, SP

A R Q . R E S P O N S Á V E L

Lidiane Barbosa
CAU A290220-6

A R Q . C O R R E S P O N S Á V E L

Isadora Ferrari
CAU A269382-8

D A T A

26/09/2026

R E V I S Ã O

Nº 00

E S C A L A


1/50

CONFERIR AS MEDIDAS NO LOCAL

Elevações — Banheiros


E04 Banheiro Casal — box planejado

vista de dentro, olhando o fundo do box · 1/50

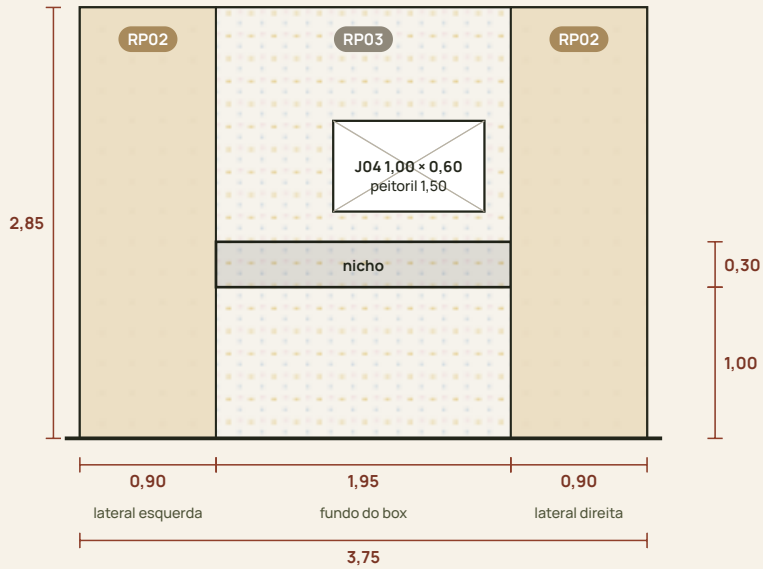


E05 WC 02 — box planejado

vista de dentro, olhando o fundo do box · 1/50

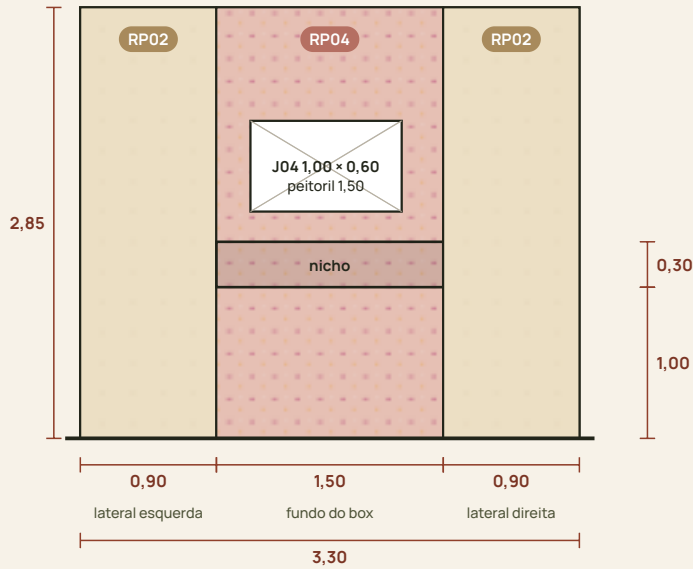

E06 WC 01 — box planejado

vista de dentro, olhando o fundo do box · 1/50

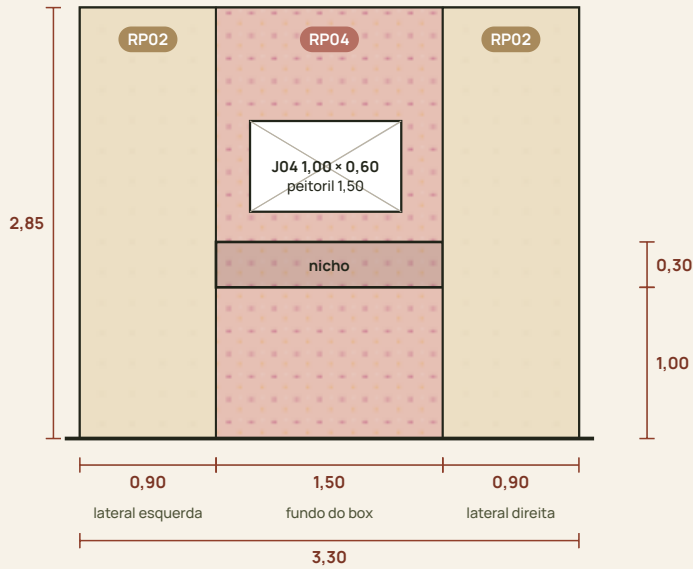

E07 Banheiro Externo — box planejado

vista de dentro, olhando o fundo do box · 1/50

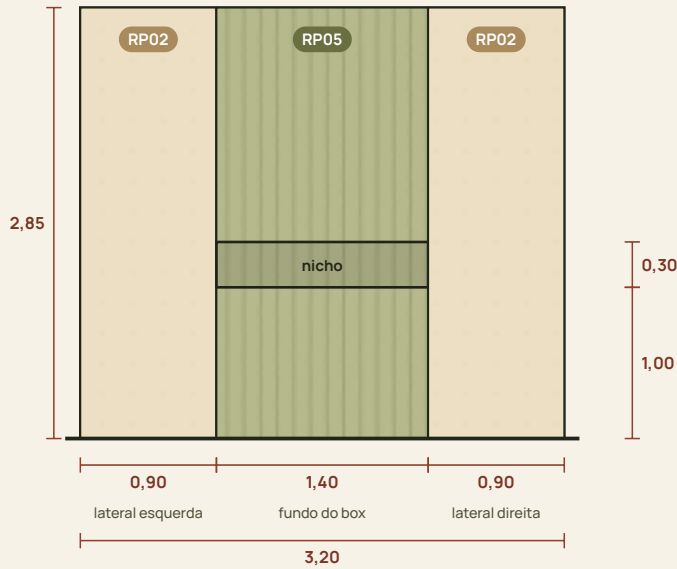


Imagem de referência · WC 01 / WC 02 — ilustrativa; valem as cotas e o quadro.

Divergência: a imagem mostra peças pequenas no Confete Pink; especificado 100 x 100 cm conforme o link informado — confirmar o formato.



Imagem de referência · Banheiro Externo — ilustrativa; valem as cotas e o quadro.

Divergência: a imagem mostra porcelanato no fundo do box; especificado Fatto Oliva, conforme informado.


NOTAS

Box Planificado: lateral esquerda + fundo + lateral direita, vistos de dentro. Laterais: 0,90 m de Santorini (RP02).

Nicho Em toda a largura da parede da janela; no Banheiro Externo, no fundo do box. 0,30 x 0,10 m, base a 1,00 m.

J04 Janela 1,00 x 0,60 m, peitoril 1,50 m (Quadro de Esquadrias Rev. 01).

CORTE DO NICHOS · AMPLIAÇÃO 1/10

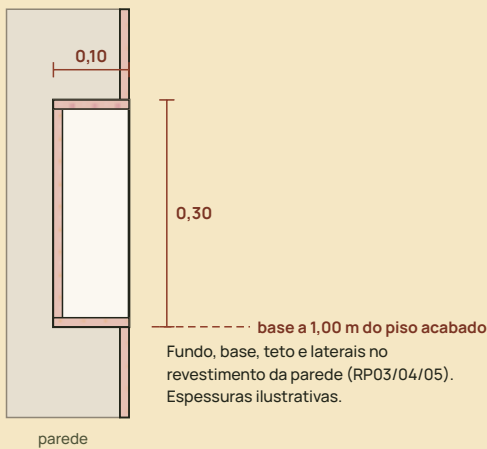

ESCALA 1/50



duas
design
& arq

FOLHA

04/05

CADERNO DE DETALHAMENTO DE REVESTIMENTO DE PAREDE 02/02

TIPO

Elevações — Banheiros

OBRA

Design de interiores de casa unifamiliar térrea

CLIENTES

Ivan e Carol

ENDEREÇO

Nova Odessa, SP

ARQ. RESPONSÁVEL

Lidiane Barbosa
CAU A290220-6

ARQ. CORRESPONSÁVEL

Isadora Ferrari
CAU A269382-8

DATA

26/09/2026

REVISÃO

Nº 00

ESCALA


1/50

CONFERIR AS MEDIDAS NO LOCAL

Elevações — Cozinha, Lavanderia e Varanda

E09 Cozinha — paredes esquerda e superior

planificadas no canto · 1/50 · desconta a janela J02

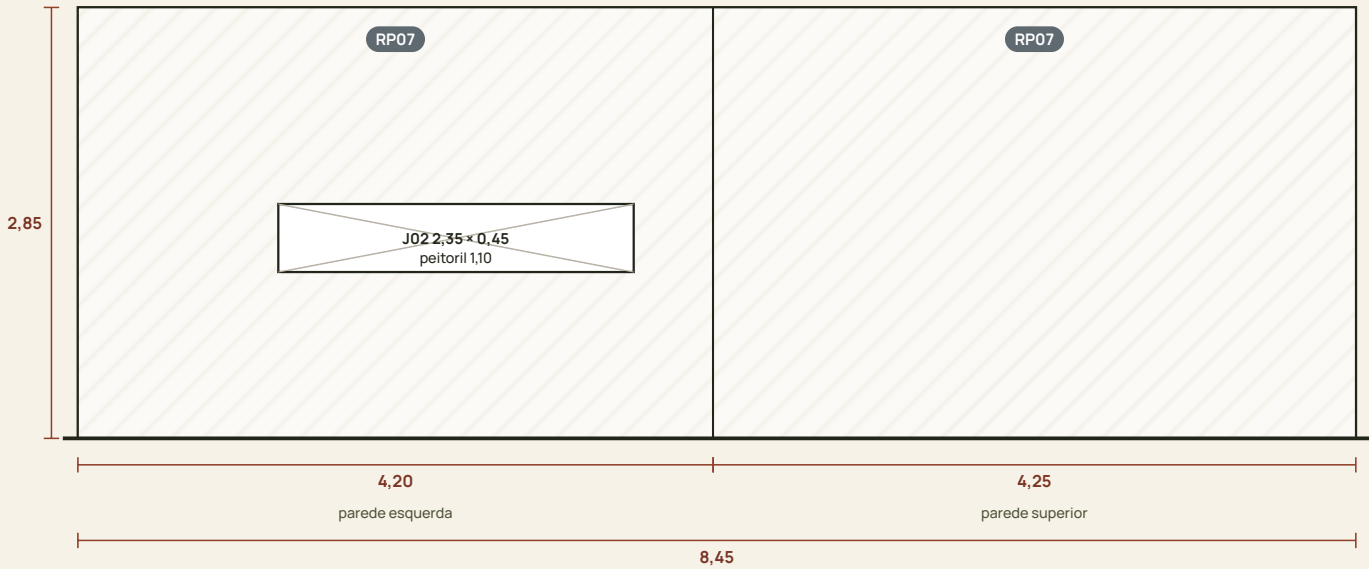


E10 Cozinha — balcão (mureta)

faces sul e norte iguais · 1/50 · mureta 1,90 × 0,15 m, h 1,00 m




E11 Varanda Gourmet — parede esquerda e churrasqueira

vista de dentro · 1/50 · faixa junto à churrasqueira

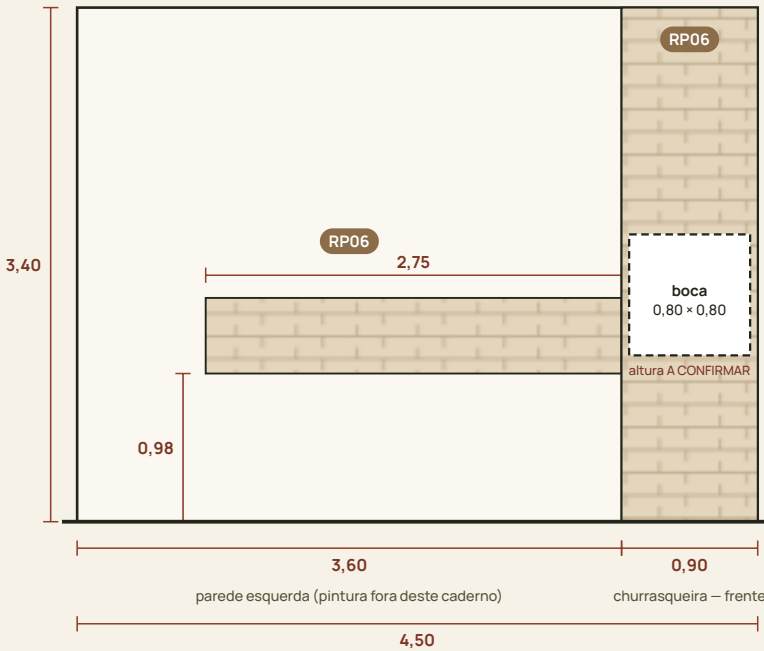

E12 Churrasqueira — lateral esquerda

vista de dentro · 1/50

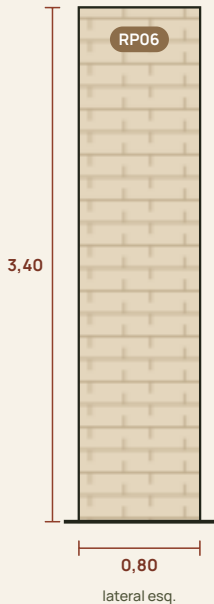

E08 Lavanderia — parede inferior

vista de dentro · 1/50 · parede inteira

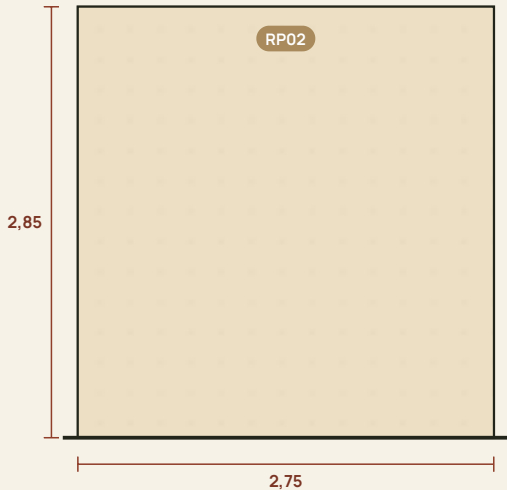


Imagem de referência · Varanda Gourmet — ilustrativa; valem as cotas e o quadro.



Imagem de referência · Lavanderia — ilustrativa; valem as cotas e o quadro.
Divergência: a imagem mostra revestimento só entre bancada e armário; especificada a parede inteira, conforme informado.

PENDÊNCIAS

- Fatto Oliva (Banheiro Externo) e cerâmica simples (Cozinha): altura adotada = PD 2,85 m — confirmar.
- Churrasqueira: altura de instalação da boca 0,80 × 0,80 (desenhada em posição indicativa).
- Rodapé × revestimento até o piso: nos trechos revestidos dos banheiros, lavanderia, cozinha e parede da TV, o Caderno 01/02 prevê rodapé R01 (≈ 28,35 m). Confirmar se o rodapé sai desses trechos.
- Churrasqueira (0,90 × 0,80 m) ocupa 0,72 m² do piso P02 da Varanda e trechos de rodapé R02 — o Caderno 01/02 não desconta. Confirmar a atualização.
- Fachada sul: pano inclui a face do pilar junto à garagem (0,15 m), conforme imagem — conferir.
- Parede da TV: largura pela geometria do DWG = 3,60 m (imagem cota 3,75 m); altura = PD 3,40 m do DWG (imagem cota 3,591 m).
- Banheiro Externo: o quadro de esquadrias indica J06 sobre P11 (outra parede); o nicho segue o fundo do box, conforme informado.
- Balcão: revestidas apenas as duas faces de 1,90 × 1,00 m; topo e cabeceiras (0,15 m) sem revestimento — confirmar. Mureta só consta no DWG da Prefeitura.
- Moledo e Travertino Rock Face (pedreira): formato, espessura, assentamento e rejunte A CONFIRMAR. Confete WH e Fatto Oliva: rejunte e espessura A CONFIRMAR na ficha.
- Imagens de referência: divergências anotadas nas folhas 03 a 05 (formato do Confete Pink, fundo do box do Banheiro Externo, extensão na Lavanderia).
- Paginação não faz parte deste caderno. Quantitativos líquidos, sem perdas de compra. Conferir todas as medidas no local.

ESCALA 1 / 50



FOLHA

05/05

CADERNO DE DETALHAMENTO DE REVESTIMENTO DE PAREDE 02/02

TIPO

Elevações — Cozinha, Lavanderia e Varanda

OBRA

Design de interiores de casa unifamiliar térrea

CLIENTES

Ivan e Carol

ENDEREÇO

Nova Odessa, SP

ARQ. RESPONSÁVEL

Lidiane Barbosa
CAU A290220-6

ARQ. CORRESPONSÁVEL

Isadora Ferrari
CAU A269382-8

DATA

26/09/2026

REVISÃO

Nº 00

ESCALA

1/50

CONFERIR AS MEDIDAS NO LOCAL