

Pisos

CÓD.	PRODUTO	ÁREA
P01	Porcelanato Santorini OFW NAT	197,67
P02	Porcelanato Santorini SGR HARD	96,01
PP01	Pedra portuguesa branca	150,10
-	Corredor Lateral Externo — P02 ou PI01 (a definir)	23,93
Total geral		467,71

Rodapés

CÓD.	RODAPÉ (H = 8 CM)	LÍQUIDO
R01	Santorini OFW NAT — mesmo piso P01	159,10
R02	Santorini SGR HARD — mesmo piso P02	30,04
Total		189,14

Trechos e memória de cálculo nas folhas 03/06 e 04/06. Sem rodapé em PP01 e no Corredor Lateral Externo.

duas design & arq

FOLHA

01/06

CADERNO DE DETALHAMENTO DE REVESTIMENTO DE PISO 01/02

TIPO

Planta de especificação de pisos

OBRA

Design de interiores de casa unifamiliar térrea

CLIENTES

Ivan e Carol

ENDEREÇO

Nova Odessa, SP

ARQ. RESPONSÁVEL

Lidiane Barbosa
CAU A290220-6

ARQ. CORRESPONSÁVEL

Isadora Ferrari
CAU A269382-8

DATA

26/09/2026

REVISÃO

Nº 00

ESCALA

1/125


CONFERIR AS MEDIDAS NO LOCAL

LEGENDA

- P01 Santorini OFW NAT
90 × 90
- P02 Santorini SGR
HARD 90 × 90
- PP01 Pedra portuguesa
branca
- A definir: P02 ou PI01
(intertravado
drenante)
- Área verde (sem piso)
- Piscina
- Transição de piso
(folha 05/06)
- Soleira mármore
Itaúnas, baguete 5 cm
(detalhe D3)
- Vão de porta
- Divisa do lote

ESCALA

1/125

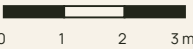

Imprimir em A3 sem ajuste de escala.

² Quarto Casal e Closet Casal pela geometria do DWG (16,28 + 12,25 = 28,53 m²). No quadro, o conjunto adota 28,70 m² (maior valor, Prefeitura).

Quadro de pisos

CÓD.	AMBIENTE	PRODUTO	FABRICANTE	FORMATO	ACABAMENTO	REJUNTE	ÁREA M²	CONTROLE	
P01 · PORCELANATO SANTORINI OFW NAT – PORTINARI									
P01	Quarto Casal + Closet Casal	Porcelanato Santorini OFW NAT	Portinari	90 × 90 cm	Natural (NAT)	Corda · junta seca	28,70	Arquivo	Informado
P01	Banheiro Casal	Porcelanato Santorini OFW NAT	Portinari	90 × 90 cm	Natural (NAT)	Corda · junta seca	6,83	Arquivo	
P01	Quarto 01	Porcelanato Santorini OFW NAT	Portinari	90 × 90 cm	Natural (NAT)	Corda · junta seca	12,30	Arquivo	Informado
P01	WC 01	Porcelanato Santorini OFW NAT	Portinari	90 × 90 cm	Natural (NAT)	Corda · junta seca	4,20	Arquivo	Informado
P01	Quarto 02	Porcelanato Santorini OFW NAT	Portinari	90 × 90 cm	Natural (NAT)	Corda · junta seca	12,30	Arquivo	Informado
P01	WC 02	Porcelanato Santorini OFW NAT	Portinari	90 × 90 cm	Natural (NAT)	Corda · junta seca	4,20	Arquivo	Informado
P01	Escritório	Porcelanato Santorini OFW NAT	Portinari	90 × 90 cm	Natural (NAT)	Corda · junta seca	7,26	Arquivo	Informado
P01	Banheiro Externo	Porcelanato Santorini OFW NAT	Portinari	90 × 90 cm	Natural (NAT)	Corda · junta seca	4,62	Arquivo	
P01	Circulação Interna (inclui nicho de marcenaria)	Porcelanato Santorini OFW NAT	Portinari	90 × 90 cm	Natural (NAT)	Corda · junta seca	12,85	Arquivo	Obra
P01	Cozinha	Porcelanato Santorini OFW NAT	Portinari	90 × 90 cm	Natural (NAT)	Corda · junta seca	17,85	Arquivo	Informado
P01	Sala TV / Sala Jantar (integradas)	Porcelanato Santorini OFW NAT	Portinari	90 × 90 cm	Natural (NAT)	Corda · junta seca	41,01	Arquivo	Informado
P01	Lavanderia	Porcelanato Santorini OFW NAT	Portinari	90 × 90 cm	Natural (NAT)	Corda · junta seca	5,50	Arquivo	Informado
P01	Depósito	Porcelanato Santorini OFW NAT	Portinari	90 × 90 cm	Natural (NAT)	Corda · junta seca	2,40	Arquivo	Informado
P01	Garagem	Porcelanato Santorini OFW NAT	Portinari	90 × 90 cm	Natural (NAT)	Corda · junta seca	37,65	Arquivo	
Subtotal P01							197,67		
P02 · PORCELANATO SANTORINI SGR HARD – PORTINARI									
P02	Varanda Gourmet	Porcelanato Santorini SGR HARD	Portinari	90 × 90 cm	HARD (antiderrapante)	Corda · junta seca	18,32	Arquivo	
P02	Deck (inclui faixas sob beiral)	Porcelanato Santorini SGR HARD	Portinari	90 × 90 cm	HARD (antiderrapante)	Corda · junta seca	77,69	Arquivo	Informado
Subtotal P02							96,01		
PP01 · PEDRA PORTUGUESA BRANCA									
PP01	Rampa de acesso à garagem	Pedra portuguesa branca	—	A CONFIRMAR	A CONFIRMAR	A CONFIRMAR	37,00	Informado	
PP01	Acesso externo lateral (até P03)	Pedra portuguesa branca	—	A CONFIRMAR	A CONFIRMAR	A CONFIRMAR	15,03	Arquivo	Obra
PP01	Calçada — faixas de acesso e livre (2,35 m)	Pedra portuguesa branca	—	A CONFIRMAR	A CONFIRMAR	A CONFIRMAR	98,07	Arquivo	Obra
Subtotal PP01							150,10		
A DEFINIR — P02 (SANTORINI SGR HARD) OU PI01 (PISO INTERTRAVADO DRENANTE)									
P02/PI01	Corredor Lateral Externo	A DEFINIR: P02 ou PI01	Portinari / A CONFIRMAR	90 × 90 cm ou A CONFIRMAR	HARD ou drenante	Corda ou A CONFIRMAR	23,93	Informado	Obra
Subtotal a definir (P02 ou PI01)							23,93		
TOTAL GERAL (P01 + P02 + PP01 + a definir) — cada ambiente contado uma vez							467,71		

ESPECIFICAÇÃO DOS PORCELANATOS — DADOS DO FABRICANTE

P01	Santorini OFW NAT 90 × 90								
DESCRIÇÃO	Porcelanato esmaltado Santorini OFW NAT (Off White), borda retificada								
FABRICAÇÃO	900 × 900 mm · espessura 7,0 mm · monocalibre								
EMBALAGEM	3 peças / 2,43 m² por caixa								
USO	áreas internas (Cód. Portinari, variação V e classe de uso: A CONFIRMAR na ficha)								
JUNTA	junta seca (fabricante)								
REJUNTE	cor Corda (sugerida pelo fabricante) · proposta: argamassa de rejuntamento tipo II, NBR 14992, em WCs, banheiros, cozinha e lavanderia; tipo I nas áreas secas								

P02	Santorini SGR HARD 90 × 90								
DESCRIÇÃO	Porcelanato esmaltado Santorini SGR HARD (Stone Gray, cinza), cód. 62928, borda retificada								
FABRICAÇÃO	900 × 900 mm · espessura 8,0 mm · monocalibre								
EMBALAGEM	2 peças / 1,62 m² por caixa								
USO	USO 6 (residencial e comercial de tráfego intenso) · variação V3 · interno e externo								
JUNTA	junta seca (fabricante)								
REJUNTE	cor Corda (sugerida pelo fabricante) · proposta: argamassa de rejuntamento tipo II, NBR 14992 (área externa)								

CRITÉRIOS

- 1

Dados técnicos dos porcelanatos pelos links do fabricante informados pela arquitetura (Portinari). Conferir na ficha técnica vigente antes da compra.
- 2

Rejunte: cor Corda e junta seca, conforme o fabricante. O tipo da argamassa de rejuntamento (NBR 14992) é proposta e depende da aprovação da arquitetura.
- 3

Áreas pela face interna das paredes, sem soleiras. Nas divergências entre documentos, adotado o maior valor.
- 4

Deck com as faixas de 1,00 m sob o beiral. Piscina não pavimentada.
- 5

Calçada: faixas 1,25 + 1,10 = 2,35 m, sem o meio-fio (com ele: 104,54 m²). Término junto à Av. 3 A CONFIRMAR. Rampa: valor informado; pela geometria, 34,61 m².
- 6

Quantitativos líquidos, sem perdas de compra. Níveis não considerados.

Controle dos dados: Arquivo confirmado no arquivo · Informado informado pela arquitetura · Obra conferir em obra · Decisão decisão da arquitetura.



duas
design
& arq

FOLHA

02/06

CADERNO DE DETALHAMENTO DE REVESTIMENTO DE
PISO 01/02

T I P O

Quadro de pisos

OBRA
Design de interiores de casa unifamiliar térrea

CLIENTES
Ivan e Carol

ENDEREÇO
Nova Odessa, SP

ARQ. RESPONSÁVEL
Lidiane Barbosa
CAU A290220-6

ARQ. CORRESPONSÁVEL
Isadora Ferrari
CAU A269382-8

DATA
26/09/2026

REVISÃO
Nº 00

ESCALA
Sem escala

CONFERIR AS MEDIDAS NO LOCAL

LEGENDA

- R01** Rodapé Santorini
OFW NAT, h = 8 cm

- R02** Rodapé Santorin
SGR HARD, h = 8 cm

- Início / fim de trecho de rodapé


- Vão de porta
descontado – largura
do DWG (m)

- ☐ Face de parede sem rodapé


O rodapé é do mesmo revestimento do piso do ambiente onde está instalado. Janelas não são descontadas.

ESCALA

1/100

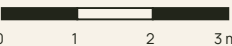

Imprimir em A3 sem ajuste de escala.

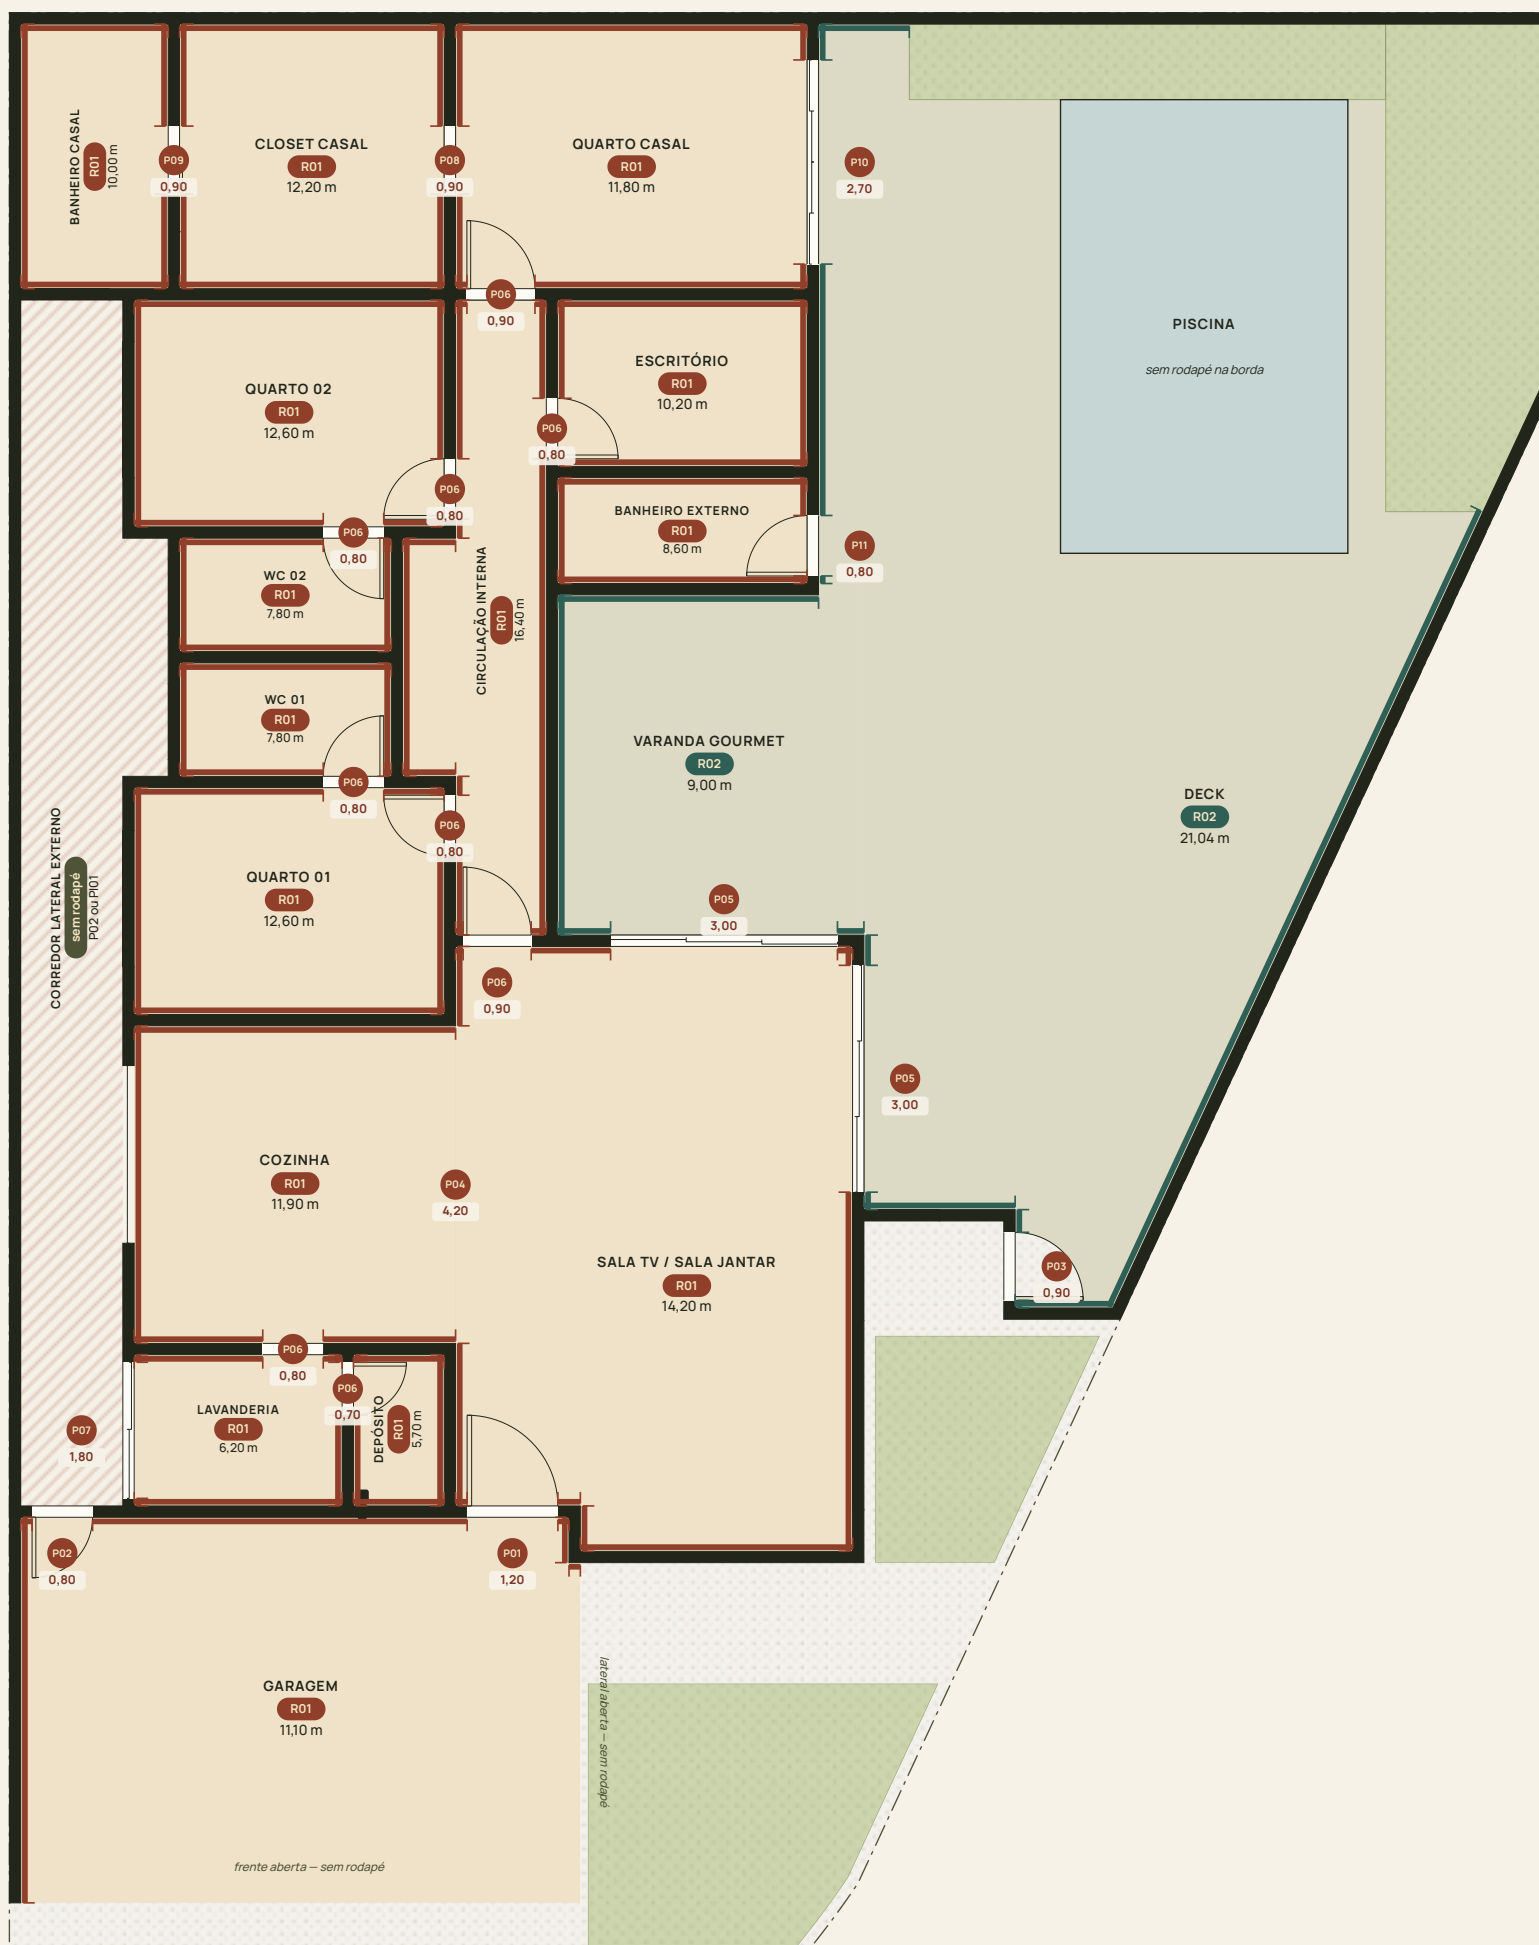

Vãos descontados

medidas em metros

CÓD.	VÃO DWG	QUADRO ESQ.	QTD.
P01	1,20	1,20	1
P02	0,80	0,90	1
P03	0,90	0,90	1
P04	4,20	4,20	1
P05	3,00	3,00	2
P06	0,70 / 0,80 / 0,90	0,90	9
P07	1,80	1,80	1
P08	0,90	1,00	1
P09	0,90	1,00	1
P10	2,70	2,50	1
P11	0,80	0,90	1

Rodapés

metros lineares

CÓD.	RODAPE (H = 8 CM)	LÍQUIDO
R01	Santorini OFW NAT	159,10
R02	Santorini SGR HARD	30,04
Total		189,14

Descontos pelos vãos do DWG (orientação da arquitetura). Em vermelho, vão do DWG diferente do Quadro de Esquadrias Rev. 01. P04 (4,20) não está desenhada no DWG: largura informada



CADERNO DE DETALHAMENTO DE REVESTIMENTO D
PISO 01/02

TIP O

Planta de rodapés

OBRA

Design de interiores de casa unifamiliar térrea

CLIENTES
Ivan e Caro

ARQ. RESPONSÁVEL
Lidiane Barbosa
CAU A290220-6

DATA
26/09/2026

ENDEREÇO
Nova Odessa, SP

ARQ. CORRESPONSÁVEL
Isadora Ferrari
CAU A269382-8

REVISÃO
Nº 00

ESCALA
1/100

ESCALA
1/100

CONFERIR AS MEDIDAS NO LOCA

Memória de cálculo dos rodapés

CÓD.	AMBIENTE	TRECHOS DE PAREDE (M) – POSIÇÃO NA PLANTA	SOMA	VÃOS DE PORTA DESCONTADOS (DWG)	VÃOS	LÍQUIDO	CONTROLE
R 01 · RODAPÉ PORCELANATO SANTORINI OFW NAT · H = 8 CM							
R01	Quarto Casal	inf. 4,65 + dir. 3,50 + sup. 4,65 + esq. 3,50	16,30	P06 0,90 + P10 2,70 + P08 0,90	4,50	11,80	Arquivo
R01	Closet Casal Trechos atrás de marcenaria: conferir com o projeto de marcenaria	inf. 3,50 + dir. 3,50 + sup. 3,50 + esq. 3,50	14,00	P08 0,90 + P09 0,90	1,80	12,20	Arquivo
R01	Banheiro Casal	inf. 1,95 + dir. 3,50 + sup. 1,95 + esq. 3,50	10,90	P09 0,90	0,90	10,00	Arquivo
R01	Quarto 02	inf. 4,10 + dir. 3,00 + sup. 4,10 + esq. 3,00	14,20	P06 0,80 + P06 0,80	1,60	12,60	Arquivo
R01	WC 02	inf. 2,80 + dir. 1,50 + sup. 2,80 + esq. 1,50	8,60	P06 0,80	0,80	7,80	Arquivo
R01	WC 01	inf. 2,80 + dir. 1,50 + sup. 2,80 + esq. 1,50	8,60	P06 0,80	0,80	7,80	Arquivo
R01	Quarto 01	inf. 4,10 + dir. 3,00 + sup. 4,10 + esq. 3,00	14,20	P06 0,80 + P06 0,80	1,60	12,60	Arquivo
R01	Escritório	inf. 3,30 + dir. 2,20 + sup. 3,30 + esq. 2,20	11,00	P06 0,80	0,80	10,20	Arquivo
R01	Banheiro Externo	inf. 3,30 + dir. 1,40 + sup. 3,30 + esq. 1,40	9,40	P11 0,80	0,80	8,60	Arquivo
R01	Circulação Interna Nicho (futura marcenaria) com piso e rodapé, conforme informado	inf. 1,20 + dir. 8,40 + sup. 1,20 + esq. sup. 3,15 + nicho sup. 0,70 + nicho esq. 3,15 + nicho inf. 0,70 + esq. inf. 2,10	20,60	P06 0,90 + P06 0,80 + P06 0,90 + P06 0,80 + P06 0,80	4,20	16,40	Arquivo Informado
R01	Cozinha	inf. 4,25 + dir. 4,20 + sup. 4,25 + esq. 4,20	16,90	P06 0,80 + P04 4,20	5,00	11,90	Arquivo Informado
R01	Lavanderia	inf. 2,75 + dir. 2,00 + sup. 2,75 + esq. 2,00	9,50	P06 0,80 + P06 0,70 + P07 1,80	3,30	6,20	Arquivo
R01	Depósito	inf. 1,20 + dir. 2,00 + sup. 1,20 + esq. 2,00	6,40	P06 0,70	0,70	5,70	Arquivo
R01	Sala TV / Sala Jantar J01 (peitoril 0,50) não descontada	inf. esq. 1,65 + recuo 0,60 + inf. dir. 3,60 + dir. 8,00 + sup. 5,25 + esq. 7,40	26,50	P01 1,20 + P05 3,00 + P05 3,00 + P06 0,90 + P04 4,20	12,30	14,20	Arquivo Informado
R01	Garagem Frente (7,40) e lateral direita (4,50) abertas no DWG: sem rodapé	esq. 5,10 + sup. 7,25 + pilar dir. 0,60 + pilar inf. 0,15	13,10	P02 0,80 + P01 1,20	2,00	11,10	Arquivo
Subtotal R01						159,10	
R 02 · RODAPÉ PORCELANATO SANTORINI SGR HARD · H = 8 CM							
R02	Varanda Gourmet Lado direito aberto para o deck: sem rodapé	inf. 4,05 + esq. 4,50 + sup. 3,45	12,00	P05 3,00	3,00	9,00	Arquivo
R02	Deck (inclui faixas sob beiral) Sem rodapé junto à piscina e às áreas verdes	fachada Q. Casal/Escr./B. Ext. 7,40 + muro sup. 1,20 + fachada Sala 3,63 + muro inf. 2,00 + portão P03 + batentes 1,30 + muro portão 1,29 + muro de divisa (diag.) 11,61	28,44	P10 2,70 + P11 0,80 + P05 3,00 + P03 0,90	7,40	21,04	Arquivo Informado
Subtotal R02						30,04	
TOTAL GERAL DE RODAPÉS (R01 + R02)						189,14	

REGRA DE CÁLCULO

- 1

Rodapé líquido = soma dos trechos de parede – vãos de porta aplicáveis. Janelas não são descontadas. Cada face de parede entra uma única vez; as duas faces de uma mesma parede pertencem a ambientes diferentes.
- 2

Material do rodapé = piso do ambiente: P01 → R01 (Santorini OFW NAT); P02 → R02 (Santorini SGR HARD). Altura 8 cm (informada), rejunte igual ao do piso. Sem rodapé em PP01 (rampa, acesso externo e calçada) e no Corredor Lateral Externo.
- 3

Trechos sem rodapé: faces abertas da garagem (frente 7,40 e lateral 4,50), lado aberto da varanda, bordas da piscina e limites com áreas verdes.
- 4

Vãos pelo DWG (orientação da arquitetura). P04 (4,20) não está no DWG: descontada como passagem entre Cozinha e Sala, conforme informado. Com as larguras do Quadro de Esquadrias Rev. 01 o líquido de R01 seria 157,10 m e o de R02, 30,14 m.
- 5

Circulação Interna: inclui o nicho de 0,70 × 3,15 m (futura marcenaria), com piso e rodapé, conforme informado.
- 6

Metros lineares líquidos, sem perdas de corte ou de compra.

Controle dos dados: Arquivo confirmado no arquivo · Informado informado pela arquitetura · Obra conferir em obra · Decisão decisão da arquitetura.



duas
design
& arq

FOLHA

04/06

CADERNO DE DETALHAMENTO DE REVESTIMENTO DE PISO 01/02

T I P O

Memória de cálculo dos rodapés

OBRA
Design de interiores de casa unifamiliar térrea

CLIENTES
Ivan e Carol

ENDEREÇO
Nova Odessa, SP

ARQ. RESPONSÁVEL
Lidiane Barbosa
CAU A290220-6

ARQ. CORRESPONSÁVEL
Isadora Ferrari
CAU A269382-8

DATA
26/09/2026

REVISÃO
Nº 00

ESCALA
Sem escala

CONFERIR AS MEDIDAS NO LOCAL

Transições e pendências

CÓD.	PORTA	ENCONTRO DE PISOS	SOLUÇÃO	SOLEIRA M	CONTROLE
T01	P02	Garagem (P01) / Corredor Lateral Externo (P02 ou PI01)	Soleira mármore Itaúnas, baguete 5 cm × comprimento do vão (0,80 m).	0,80	Informado
T02	P07	Lavanderia (P01) / Corredor Lateral Externo (P02 ou PI01)	Soleira mármore Itaúnas, baguete 5 cm × comprimento do vão (1,80 m). Compatibilizar com o trilho embutido (esquadrias, notas 3 e 10).	1,80	Informado
T03	P05	Sala TV / Sala Jantar (P01) / Varanda Gourmet (P02)	Soleira mármore Itaúnas, baguete 5 cm × comprimento do vão (3,00 m). Compatibilizar com o trilho embutido.	3,00	Informado
T04	P05	Sala TV / Sala Jantar (P01) / Deck (P02)	Soleira mármore Itaúnas, baguete 5 cm × comprimento do vão (3,00 m). Compatibilizar com o trilho embutido.	3,00	Informado
T05	P10	Quarto Casal (P01) / Deck (P02)	Soleira mármore Itaúnas, baguete 5 cm × comprimento do vão (2,70 m). Compatibilizar com o trilho da veneziana de correr.	2,70	Informado
T06	P11	Banheiro Externo (P01) / Deck (P02)	Soleira mármore Itaúnas, baguete 5 cm × comprimento do vão (0,80 m).	0,80	Informado
T07	P03	Deck (P02) / Acesso externo (PP01)	Soleira mármore Itaúnas, baguete 5 cm × comprimento do vão (0,90 m).	0,90	Informado
T08	—	Garagem (P01) / Rampa (PP01) — frente aberta	Soleira mármore Itaúnas, baguete 5 cm × comprimento do vão (7,40 m, linha y = 15,036).	7,40	Informado
T09	—	Garagem (P01) / Acesso externo (PP01) — lateral aberta	Soleira mármore Itaúnas, baguete 5 cm × comprimento do vão (4,50 m).	4,50	Informado
T10	—	Deck (P02) / Piscina	Borda da piscina e arremate não documentados: A CONFIRMAR.	—	Decisão
T11	—	Deck (P02) e PP01 / áreas verdes	Contenção/arremate entre piso e jardim não documentado: A CONFIRMAR.	—	Decisão
T12	—	Rampa (PP01) / Calçada (PP01) — divisa	Mesmo material: sem soleira. Havendo desnível: perfil metálico (mesmo material, somente com desnível).	—	Informado
T13	P04	Cozinha (P01) / Sala TV / Sala Jantar (P01)	Mesmo material: sem soleira. Havendo desnível: perfil metálico (mesmo material, somente com desnível). Posição do trilho de P04 A CONFIRMAR.	—	Informado
T14	P06/P08/P09	Portas internas (P01 / P01)	Mesmo material: sem soleira. Havendo desnível: perfil metálico (mesmo material, somente com desnível).	—	Informado
TOTAL DE SOLEIRAS — mármore Itaúnas, baguete 5 cm (9 trechos)				24,90	

PENDÊNCIAS — DECISÃO DA ARQUITETURA

- 1
- Corredor Lateral Externo (23,93 m², incluído no total): definir entre P02 (Santorini SGR HARD) e PI01 (piso intertravado drenante). Dimensões, espessura, cor e resistência do PI01: A CONFIRMAR (anúncio não acessível na elaboração). Sem rodapé.
- 2
- P02: o produto do link é o Santorini SGR HARD (SGR = Stone Gray, cinza), não uma versão Off White. Confirmar a cor para a varanda, o deck e o rodapé R02.
- 3
- P01 (Santorini OFW NAT): confirmar na ficha técnica o código Portinari, a variação de tonalidade e a classe de uso (as fontes consultadas divergem entre USO 5 e USO 6).
- 4
- Rejunte: aprovar o tipo proposto (NBR 14992 tipo II em áreas externas e molhadas; tipo I em áreas secas), a marca e a largura da junta, conforme o manual de assentamento Portinari.
- 5
- PP01: formato/granulometria da pedra portuguesa branca, assentamento e rejunte.
- 6
- Calçada: término junto à Av. 3 (linhas abertas no DWG). A Prefeitura indica concreto vassourado na faixa de acesso e grama na faixa de serviço; confirmar a exigência municipal.
- 7
- Acesso externo lateral (15,03 m²): a Prefeitura indica concreto vassourado; a planta do caderno de esquadrias mostra grama com pisantes. Confirmar o limite da pedra portuguesa.
- 8
- Rodapé em áreas molhadas: compatibilizar com o Caderno 02/02 (revestimento de parede).
- 9
- Soleiras de mármore × trilhos embutidos de P05, P07 e P10, e posição do trilho de P04 (não desenhada no DWG).
- 10
- Borda da piscina e arremates entre piso e jardim — não documentados.

PENDÊNCIAS — CONFERÊNCIA EM OBRA

- 11
- Vãos executados × vãos do DWG × Quadro de Esquadrias Rev. 01: 13 das 20 portas têm largura diferente. Descontos de rodapé e comprimentos de soleira pelo DWG.
- 12
- Áreas divergentes adotadas pelo maior valor: Quarto Casal + Closet 28,70; Banheiro Casal 6,83; Banheiro Externo 4,62; Circulação 12,85; Garagem 37,65; Varanda 18,32; Rampa 37,00; Corredor Lateral Externo 23,93.
- 13
- Rampa: limite direito considerado no alinhamento da garagem; há guia/muro 0,10 m adiante.
- 14
- Rodapé atrás de marcenaria (closet, nicho da circulação, armários): conferir com o projeto de marcenaria.
- 15
- Tubeamento junto à parede superior da garagem: recortar o rodapé em obra.
- 16
- Todas as medidas devem ser conferidas no local antes da compra.

CRITÉRIOS DE TRANSIÇÃO (INFORMADOS PELA ARQUITETURA)

- 1
- Mesmo produto/material, apenas com mudança de nível: perfil metálico.
- 2
- Troca de material: soleira de mármore Itaúnas, tipo baguete, com 5 cm de profundidade pelo comprimento do vão.
- 3
- Níveis não documentados neste caderno. Onde houver desnível entre pisos iguais, aplicar o critério 1.
- 4
- Detalhes ilustrativos: perfil metálico (D2), soleira baguete (D3) e trilho embutido (D4) na folha 06/06.

OBSERVAÇÕES

-
- Paginação de piso não faz parte deste caderno. Revestimentos de parede: Caderno 02/02.
-
- Fonte de títulos substituída pela Outfit (Aloevera Display não disponível).

Controle dos dados: Arquivo confirmado no arquivo · Informado informado pela arquitetura · Obra conferir em obra · Decisão decisão da arquitetura.



FOLHA

05/06

CADERNO DE DETALHAMENTO DE REVESTIMENTO DE PISO 01/02

T I P O

Transições e pendências

OBRA
Design de interiores de casa unifamiliar térrea

CLIENTES
Ivan e Carol

ENDEREÇO
Nova Odessa, SP

ARQ. RESPONSÁVEL
Lidiane Barbosa
CAU A290220-6

ARQ. CORRESPONSÁVEL
Isadora Ferrari
CAU A269382-8

DATA
26/09/2026

REVISÃO
Nº 00


ESCALA
Sem escala

CONFERIR AS MEDIDAS NO LOCAL

Detalhes de rodapé e transições


D1 Rodapé em porcelanato — h = 8 cm

Corte ilustrativo · sem escala

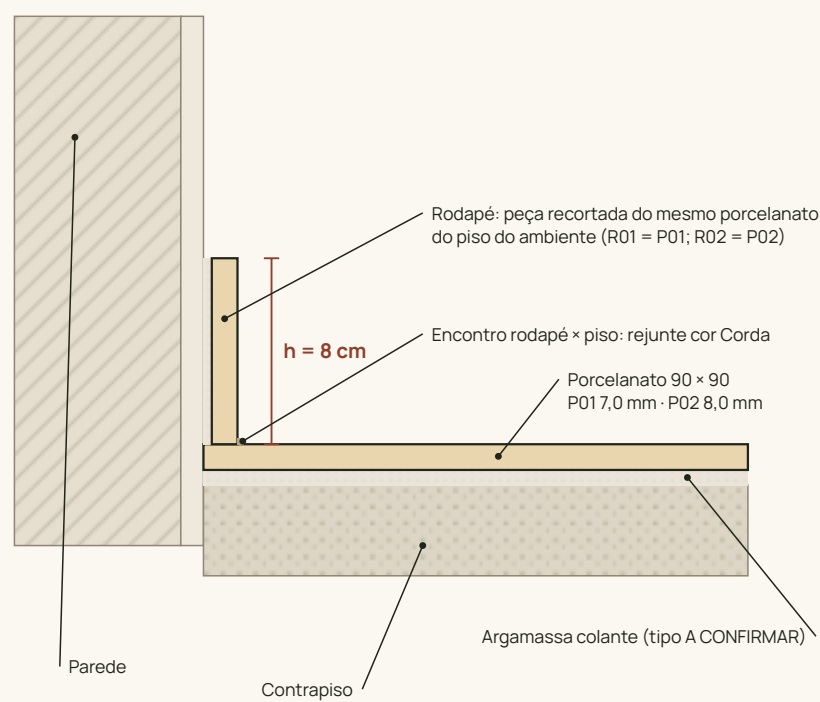

D2 Perfil metálico — mesmo material com desnível


Corte ilustrativo · sem escala

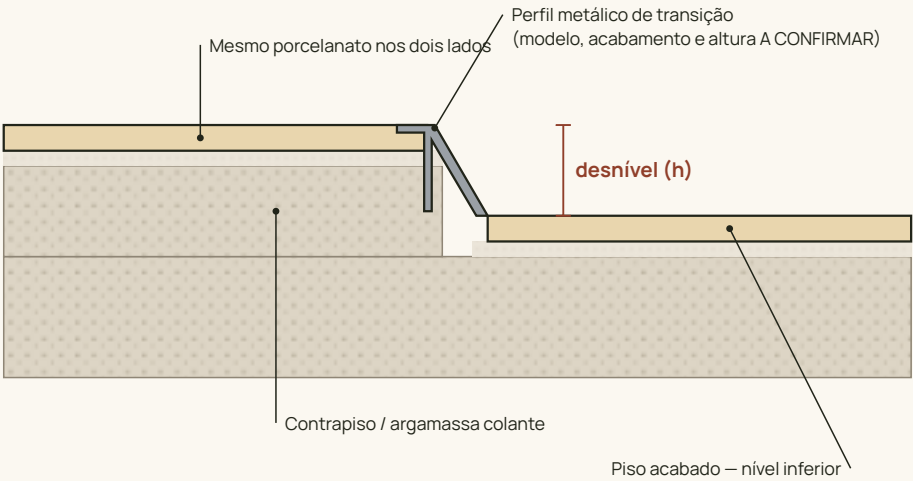


Aplicar somente quando o mesmo material mudar de nível. Níveis não documentados neste caderno.

D3 Soleira baguete — mármore Itaúnas

Corte e planta ilustrativos · sem escala

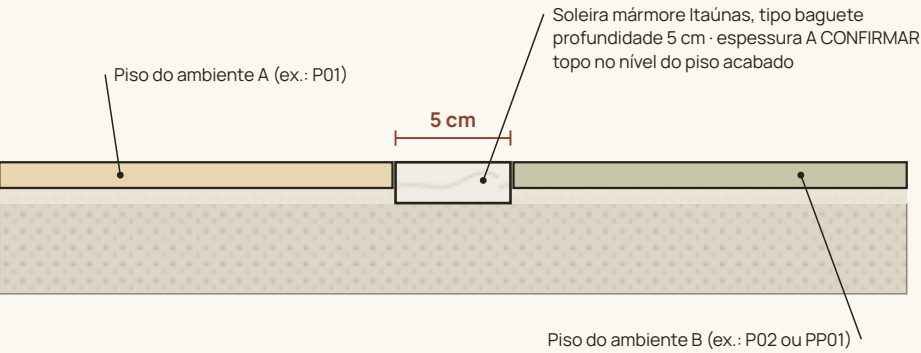


PLANTA

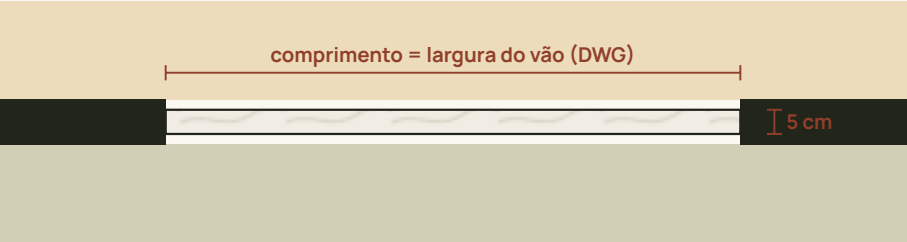

D4 Trilho de porta de correr embutido no piso

Corte ilustrativo · sem escala

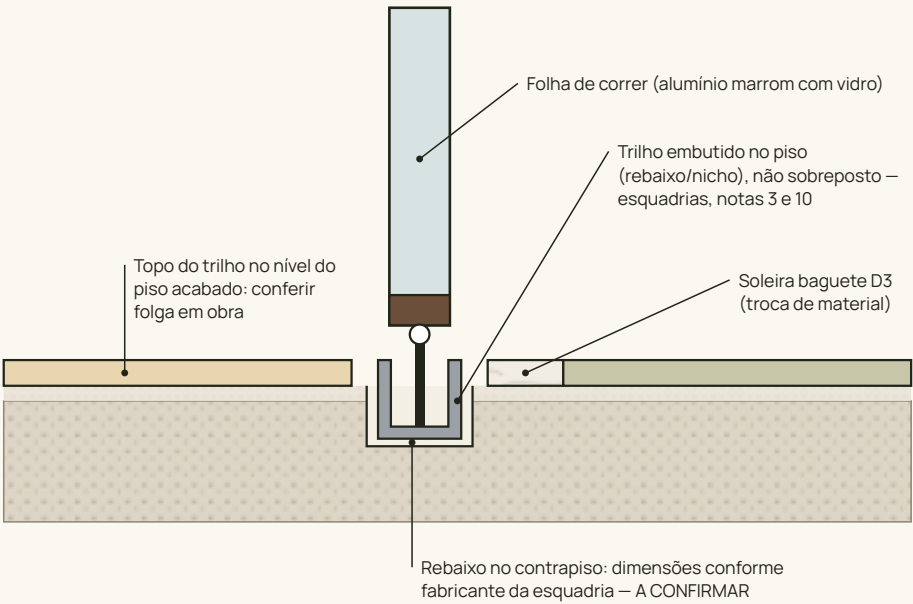

Aplica-se a P04, P05 e P07 (caderno de esquadrias), P10: tipo de trilho A CONFIRMAR. Nas portas externas, compatibilizar o trilho com a soleira baguete.

ONDE SE APLICA

- D1 Todos os rodapés R01 e R02 (folhas 03/06 e 04/06).
- D2 Encontros do mesmo material com desnível (critério 1 da folha 05/06). Níveis não documentados neste caderno.
- D3 Trocas de material T01 a T09 — 24,90 m de soleira (folha 05/06).
- D4 Portas de correr P04, P05 e P07; P10 A CONFIRMAR. Nas portas externas, compatibilizar o trilho com a soleira D3.

Desenhos ilustrativos, sem escala. Cotas indicadas: rodapé 8 cm e soleira 5 cm (informados); espessuras do porcelanato conforme o fabricante. Demais dimensões: A CONFIRMAR.



FOLHA

06/06

CADERNO DE DETALHAMENTO DE REVESTIMENTO DE PISO 01/02

T I P O

Detalhes de rodapé e transições

OBRA

Design de interiores de casa unifamiliar térrea

CLIENTES
Ivan e Carol

ENDEREÇO
Nova Odessa, SP

ARQ. RESPONSÁVEL
Lidiane Barbosa
CAU A290220-6

ARQ. CORRESPONSÁVEL
Isadora Ferrari
CAU A269382-8

DATA
26/09/2026

REVISÃO
Nº 00

ESCALA
Sem escala

CONFERIR AS MEDIDAS NO LOCAL